


## PLANIMETRÍA GENERAL - 1.ª ETAPA

ESC. 1/150

0 2 4 6 8 10 m

| CUADRO DE ÁREAS | m² |
|---|---|
| Área del terreno | 820.2 |
| Almacén de leña y garaje (existentes) | 75.7 |
| Calzada, estacionamientos, motos y GLP | 215.8 |
| Edificio: 1.er piso cerrado | 115.5 |
| Porches techados (bajo el 2.º piso) | 45.7 |
| Veredas, caminos y escalera exterior | 43.0 |
| Jardines y setos | 306.7 |
| 2.º piso: bar, SS.HH., terraza y escenario (techado parcial) | 161.2 |

**Área techada total (1.er + 2.º piso): 276.7 m²**

| CAPACIDAD (MODO RESTAURANTE) | MESAS | ASIENTOS |
|---|---|---|
| Jardines: sombrillas (mesas de 6 y 4) | 10 | 58 |
| 1.er piso: despacho y porches (mesas de 2 y 4) | 7 | 24 |
| 2.º piso: terraza (mesas de 4) y barras | 6 | 31 |
| **TOTAL MODO RESTAURANTE** | | **113** |

### LEYENDA

- Jardín (césped)
- Seto vivo tras el cerco de los frentes
- Caminos, vereda y porches (piedra o laja)
- Calzada y estacionamientos (adoquín de concreto)
- Estructuras existentes que se conservan
- Sombrilla profesional 3.00 × 3.00 m (removible)
- Árbol / palmera
- Proyección del 2.º piso (volados de 2.00 m)
- Columna metálica HSS 8x8x1/4

### NOTAS

1. Cotas en metros. Las estructuras de leña y garaje existentes se conservan; el garaje se usa por la misma calzada.
2. Las sombrillas S1 a S10 se anclan en camisas metálicas empotradas al ras del césped: se retiran en minutos para eventos (ver A-04).
3. El jardín posterior (S6 a S10) se reserva para la piscina de la 2.ª etapa (ver A-02).
4. Estacionamiento descubierto: 5 plazas (1 accesible 3.80 × 5.00 m) + 2 motos. Para eventos se coordina estacionamiento en la vía (ver A-03).

| VANO | DESCRIPCIÓN | ANCHO |
|---|---|---|
| V-1 | Portón de 2 hojas batientes (madera y acero) | 6.00 |
| P-1 | Portada principal de 2 hojas con techo de teja | 3.00 |
| P-2 | Puerta de servicio y evacuación del 2.º piso | 1.80 |
| P-3 | Salida de emergencia, barra antipánico | 1.20 |
| P-4 | Puerta de la caseta de GLP y residuos | 1.60 |

PROYECTO

**POLLERÍA CAMPESTRE**

ANTEPROYECTO - EDIFICIO DE ESTRUCTURA METÁLICA

UBICACIÓN

Jr. Rodríguez de Mendoza esq. calle lateral
Dist. San Nicolás (Mendoza) - Prov. Rodríguez de Mendoza
Departamento de Amazonas - Perú

PROPIETARIO

_____

PROFESIONAL RESPONSABLE (FIRMA Y SELLO)

Arq. / Ing. CIP N.° _____

PLANO

**PLANIMETRÍA GENERAL**

1.ª ETAPA: RESTAURANTE Y JARDINES

| ESCALA | FECHA |
|---|---|
| 1/150 | NOVIEMBRE 2026 |

ESPECIALIDAD

**ARQUITECTURA**

LÁMINA

**A-01**

1 de 10




## PLANIMETRÍA GENERAL - 2.ª ETAPA

ESC. 1/150

0 2 4 6 8 10 m

| CUADRO DE ÁREAS | m² |
|---|---|
| Área del terreno | 820.2 |
| Almacén de leña y garaje (existentes) | 75.7 |
| Calzada, estacionamientos, motos y GLP | 215.8 |
| Edificio: 1.er piso cerrado | 115.5 |
| Porches techados (bajo el 2.º piso) | 45.7 |
| Veredas, caminos y escalera exterior | 43.0 |
| Piscina, andenes, vestidores y relajo | 158.0 |
| Jardines y setos | 148.7 |
| 2.º piso: bar, SS.HH., terraza y escenario (techado parcial) | 161.2 |

**Área techada total (1.er + 2.º piso): 276.7 m²**

| CAPACIDAD (MODO RESTAURANTE) | MESAS | ASIENTOS |
|---|---|---|
| Jardines: sombrillas (mesas de 6 y 4) | 5 | 28 |
| Zona de relajo: camillas y hamacas | 5 | - |
| 1.er piso: despacho y porches (mesas de 2 y 4) | 7 | 24 |
| 2.º piso: terraza (mesas de 4) y barras | 6 | 31 |
| **TOTAL MODO RESTAURANTE** | | **83** |

## LEYENDA

- Jardín (césped)
- Seto vivo tras el cerco de los frentes
- Caminos, vereda y porches (piedra o laja)
- Calzada y estacionamientos (adoquín de concreto)
- Piscina y patera (2.ª etapa)
- Estructuras existentes que se conservan
- Sombrilla profesional 3.00 × 3.00 m (removible)
- Árbol / palmera
- Proyección del 2.º piso (volados de 2.00 m)
- Columna metálica HSS 8x8x1/4

## NOTAS

1. La piscina se separa del jardín con cerco de vidrio templado de 1.20 m; se entra solo por los vestidores, ducha y pediluvio (D.S. 007-2003-SA).
2. En la 2.ª etapa la sombrilla S6 pasa a la zona de relajo; S7 a S10 se guardan para eventos o se reubican.
3. Requiere autorización sanitaria de la DIRESA Amazonas, salvavidas en horario de uso y señalización de profundidades.

| VANO | DESCRIPCIÓN | ANCHO |
|---|---|---|
| V-1 | Portón de 2 hojas batientes (madera y acero) | 6.00 |
| P-1 | Portada principal de 2 hojas con techo de teja | 3.00 |
| P-2 | Puerta de servicio y evacuación del 2.º piso | 1.80 |
| P-3 | Salida de emergencia, barra antipánico | 1.20 |
| P-4 | Puerta de la caseta de GLP y residuos | 1.60 |

PROYECTO

**POLLERÍA CAMPESTRE**

ANTEPROYECTO - EDIFICIO DE ESTRUCTURA METÁLICA

UBICACIÓN

Jr. Rodríguez de Mendoza esq. calle lateral
Dist. San Nicolás (Mendoza) - Prov. Rodríguez de Mendoza
Departamento de Amazonas - Perú

PROPIETARIO

_____

PROFESIONAL RESPONSABLE (FIRMA Y SELLO)

Arq. / Ing. CIP N.° _____

PLANO

**PLANIMETRÍA GENERAL**

2.ª ETAPA: PISCINA, VESTIDORES Y RELAJO

| ESCALA | FECHA |
|---|---|
| 1/150 | NOVIEMBRE 2026 |

ESPECIALIDAD

**ARQUITECTURA**

LÁMINA

**A-02**

2 de 10




## CIRCULACIONES Y RUTAS DE EVACUACIÓN

ESC. 1/150

0 2 4 6 8 10 m

## LEYENDA

- Circulación vehicular (doble sentido)
- Circulación peatonal del público
- Recorridos por jardines y caminos
- Servicio: personal y proveedores (P-2)
- Leña: del almacén existente a la cocina
- Ruta de evacuación hacia la salida

| RUTA | RECORRIDO DE EVACUACIÓN | m |
|---|---|---|
| R1 | Escenario → escalera exterior → vereda → P-2 | 36 |
| R2 | Terraza → escalera principal → hall → P-1 | 23 |
| R3 | Cocina → ingreso de servicio → vereda → P-2 | 19 |
| R4 | SS.HH. → despacho → porche lateral → P-3 | 24 |
| R5 | Garaje y estacionamientos → calzada → V-1 | 24 |

Recorrido máximo admisible hasta una salida: 45 m (A.130).

| SALIDA / ESCALERA | ANCHO m | CAPAC. pers. |
|---|---|---|
| P-1 | 3.00 | 600 |
| V-1 | 6.00 | 1 200 |
| P-2 | 1.80 | 360 |
| P-3 | 1.20 | 240 |
| Escalera principal (2.º piso) | 1.20 | 150 |
| Escalera exterior (2.º piso) | 1.20 | 150 |

Capacidad: puertas 0.005 m/pers.; escaleras 0.008 m/pers. (A.130).

## NOTAS

1. La calzada de 6.00 m permite el cruce de dos vehículos y el acceso del camión de GLP y proveedores hasta la zona de carga.
2. Peatones y vehículos se separan: el público entra por P-1 (Jr. Rodríguez de Mendoza) y el servicio por P-2 (calle lateral).
3. En eventos: portón V-1 abierto y señalizado, personal de control en P-1 y luces de emergencia en caminos y escaleras.
4. Señalización de seguridad según NTP 399.010-1; extintores PQS en cada nivel y K en la cocina.

PROYECTO

**POLLERÍA CAMPESTRE**

ANTEPROYECTO - EDIFICIO DE ESTRUCTURA METÁLICA

UBICACIÓN

Jr. Rodríguez de Mendoza esq. calle lateral
Dist. San Nicolás (Mendoza) - Prov. Rodríguez de Mendoza
Departamento de Amazonas - Perú

PROPIETARIO

_____

PROFESIONAL RESPONSABLE (FIRMA Y SELLO)

Arq. / Ing. CIP N.° _____

PLANO

**CIRCULACIONES Y EVACUACIÓN**

VEHICULAR, PEATONAL, SERVICIO Y RUTAS DE ESCAPE

| ESCALA | FECHA |
|---|---|
| 1/150 | NOVIEMBRE 2026 |

| ESPECIALIDAD | LÁMINA |
|---|---|
| ARQUITECTURA | A-03 |
| | 3 de 10 |





## MODO RESTAURANTE

ESC. 1/300




## MODO EVENTO (SOMBRILLAS RETIRADAS)

ESC. 1/300

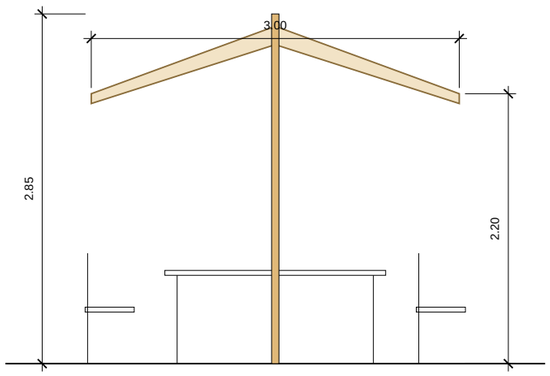



## SOMBRILLA 3.00 × 3.00 m

ESC. 1/50

## DETALLE: ANCLAJE REMOVIBLE

ESC. 1/20

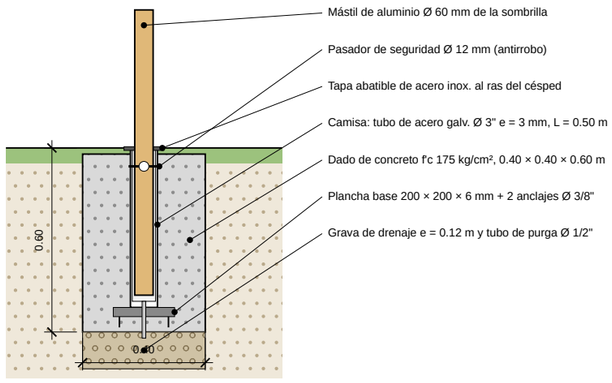


| 1.ª ETAPA | RESTAURANTE | EVENTO |
|---|---|---|
| Sombrillas 3.00 × 3.00 m instaladas | 10 | 0 |
| Asientos en jardines | 58 | 96 |
| Mesas en jardines | 10 (de 6 y 4) | 12 redondas de 8 |
| Pista de baile | - | 31.5 m² |
| Césped libre para el evento | - | 307 m² |
| Aforo de pie en jardines (1.0 m²/pers.) | - | 307 pers. |

## NOTAS

1. Cada sombrilla se ancla en una camisa empotrada en un dado de concreto bajo el césped; para un evento se retira el pasador, se levanta el mástil y se cierra la tapa al ras: el jardín queda libre en minutos y sin bases que estorben.
2. Las sombrillas retiradas se guardan cerradas en el depósito bajo la escalera o en el garaje; pueden reinstalarse en cualquier camisa o sobre bases móviles lastradas (4 × 25 kg) donde convenga.
3. Sombrilla profesional de mástil central de aluminio, lona acrílica 3.00 × 3.00 m resistente al agua y UV, con faldón; retirar o cerrar con viento > 40 km/h.
4. Modo evento: mesas redondas de 8 personas, pista de baile sobre el césped (tarima modular opcional), buffet bajo el porche lateral y la música en el escenario de la terraza.
5. En la 2.ª etapa el jardín posterior pasa a ser la zona de piscina; el modo evento usa el jardín de ingreso, el jardín lateral, los porches y la terraza.

PROYECTO

**POLLERÍA CAMPESTRE**

ANTEPROYECTO - EDIFICIO DE ESTRUCTURA METÁLICA

UBICACIÓN

Jr. Rodríguez de Mendoza esq. calle lateral
Dist. San Nicolás (Mendoza) - Prov. Rodríguez de Mendoza
Departamento de Amazonas - Perú

PROPIETARIO

_____

PROFESIONAL RESPONSABLE (FIRMA Y SELLO)

Arq. / Ing. CIP N.° _____

PLANO

**SOMBRILLAS REMOVIBLES**

MODO RESTAURANTE / MODO EVENTO Y ANCLAJE

| ESCALA | FECHA |
|---|---|
| **INDICADA** | **NOVIEMBRE 2026** |

| ESPECIALIDAD | LÁMINA |
|---|---|
| **ARQUITECTURA** | **A-04** 4 de 10 |




## PLANTA DEL 1.er PISO

ESC. 1/75

N

| AMBIENTE | m² |
|---|---|
| SS.HH. y vestidor del personal | 2.9 |
| Almacén de insumos | 4.3 |
| Ingreso de servicio | 6.6 |
| Cocina: horno pollero, parrilla y freidoras | 27.5 |
| Lavado de vajilla | 7.0 |
| Preparación fría y maceración | 6.3 |
| Cámara y bebidas | 5.9 |
| Hall de ingreso | 11.5 |
| Escalera principal | 11.4 |
| Ascensor | 3.2 |
| Despacho, caja y mesas | 13.5 |
| Lavatorios | 6.0 |
| SS.HH. accesible | 4.8 |
| SS.HH. damas | 3.5 |
| SS.HH. varones | 3.2 |
| Porches techados (bajo el 2.º piso) | 42.4 |

| CÓD. | EQUIPAMIENTO DE COCINA |
|---|---|
| HP-1, HP-2 | Hornos polleros a leña, 40 pollos c/u, con chimenea |
| PA | Parrilla a carbón 1.10 × 0.90 m |
| FR | Freidoras a gas (2), con extintor clase K |
| MT | Mesa de trabajo de acero inox. (isla) |
| PC | Pase caliente y despacho a la caja |
| LV / MM | Lavadero de 2 pozas / mesa de maceración |
| CF / DC | Conservadoras y cámara / mostrador y caja |

## NOTAS

1. Línea de fuego contra el muro de servicio bajo campana de 5.00 m (filtros, ducto y extractor); hornos con chimenea propia hasta 1.00 m sobre la cumbrera.
2. Cocina: piso antideslizante con sumidero y trampa de grasas; muros con enchape hasta 2.10 m; extintor clase K a menos de 9 m de las freidoras y extintor de agua para los hornos a leña.
3. El ascensor panorámico (cabina 1.20 × 1.40 m) y el SS.HH. accesible cumplen la Norma A.120.
4. La leña llega por la calzada desde el almacén existente hasta el ingreso de servicio.

PROYECTO

**POLLERÍA CAMPESTRE**

ANTEPROYECTO - EDIFICIO DE ESTRUCTURA METÁLICA

UBICACIÓN

Jr. Rodríguez de Mendoza esq. calle lateral
Dist. San Nicolás (Mendoza) - Prov. Rodríguez de Mendoza
Departamento de Amazonas - Perú

PROPIETARIO

_____

PROFESIONAL RESPONSABLE (FIRMA Y SELLO)

Arq. / Ing. CIP N.° _____

PLANO

**PLANTA DEL 1.er PISO**

COCINA, HORNOS, PARRILLA Y DESPACHO

| ESCALA | FECHA |
|---|---|
| 1/75 | NOVIEMBRE 2026 |

ESPECIALIDAD

**ARQUITECTURA**

LÁMINA

**A-05**

5 de 10




## PLANTA DEL 2.º PISO

ESC. 1/75

0 1 2 3 4 5 m

N

| AMBIENTE | m² |
|---|---|
| SS.HH. accesible | 5.0 |
| SS.HH. damas | 4.5 |
| SS.HH. varones | 4.2 |
| Bar y bebidas | 27.5 |
| Depósito del bar | 12.7 |
| Pasillo de servicio y evacuación | 6.6 |
| Escenario (+0.40) | 24.0 |
| Terraza exterior | 62.0 |
| Escalera principal | 11.4 |
| Ascensor | 3.2 |

| AFORO DEL 2.° PISO (A.070) | m² | PERS. |
|---|---|---|
| Terraza: restaurante (1.5 m²/pers) | 62 | 41 |
| Terraza: evento, de pie (1.0 m²/pers) | 62 | 62 |
| Bar: zona de clientes (1.0 m²/pers) | 9.7 | 10 |
| Escenario: grupo musical | 24 | 6-8 |

## NOTAS

1. Escenario de 4.00 × 6.00 m sobre tarima modular de +0.40 m; la losa se diseña para 750 kgf/m² (E.020) y puede ampliarse con módulos sobre la terraza.
2. Dos rutas de evacuación: escalera principal en U (1.20 m) y escalera exterior de 1.20 m por el pasillo de servicio; esta última sirve también para subir los equipos de sonido.
3. Barandas de vidrio laminado de 1.10 m con pasamanos de acero inoxidable.
4. Muro acústico tras el escenario y techos con aislamiento termoacústico; espectáculos hasta las 22:00 o con estudio acústico (ECA ruido).
5. Líneas grises discontinuas: proyección de los techos a dos aguas del bar y del escenario.

PROYECTO

**POLLERÍA CAMPESTRE**

ANTEPROYECTO - EDIFICIO DE ESTRUCTURA METÁLICA

UBICACIÓN

Jr. Rodríguez de Mendoza esq. calle lateral
Dist. San Nicolás (Mendoza) - Prov. Rodríguez de Mendoza
Departamento de Amazonas - Perú

PROPIETARIO

_____

PROFESIONAL RESPONSABLE (FIRMA Y SELLO)

Arq. / Ing. CIP N.° _____


PLANO

**PLANTA DEL 2.º PISO**

BAR, TERRAZA Y ESCENARIO


| ESCALA | FECHA |
|---|---|
| 1/75 | NOVIEMBRE 2026 |

| ESPECIALIDAD | LÁMINA |
|---|---|
| ARQUITECTURA | A-06 |
| | 6 de 10 |

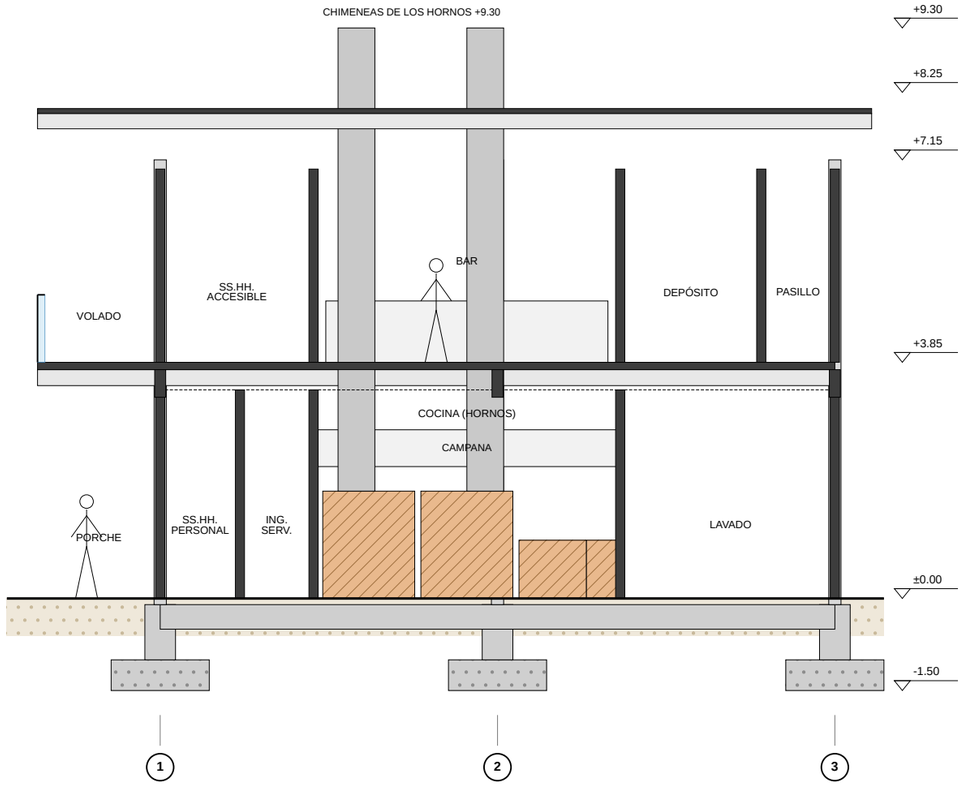



## CORTE X-X

ESC. 1/100

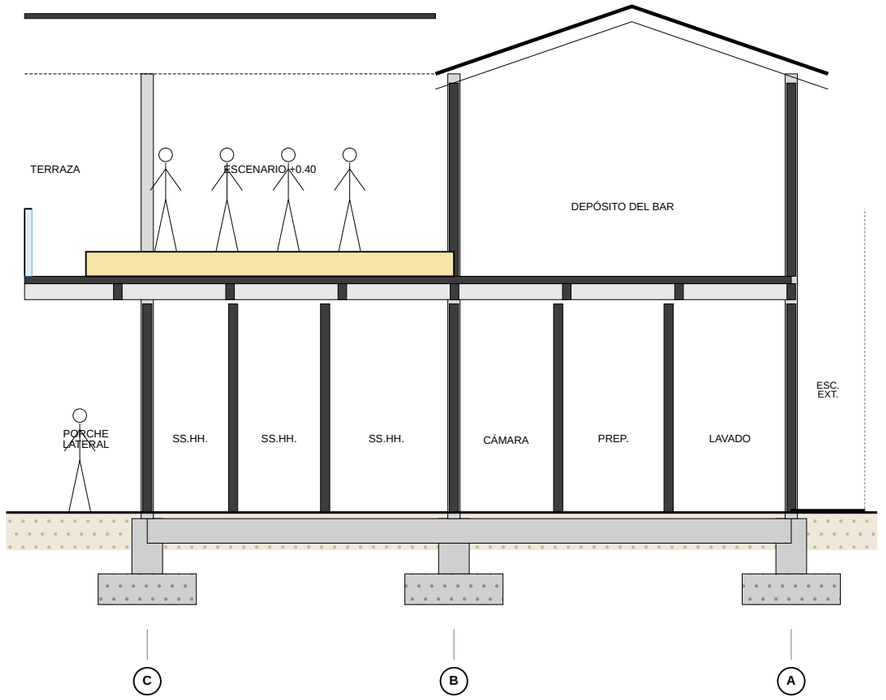



## CORTE Y-Y

ESC. 1/100

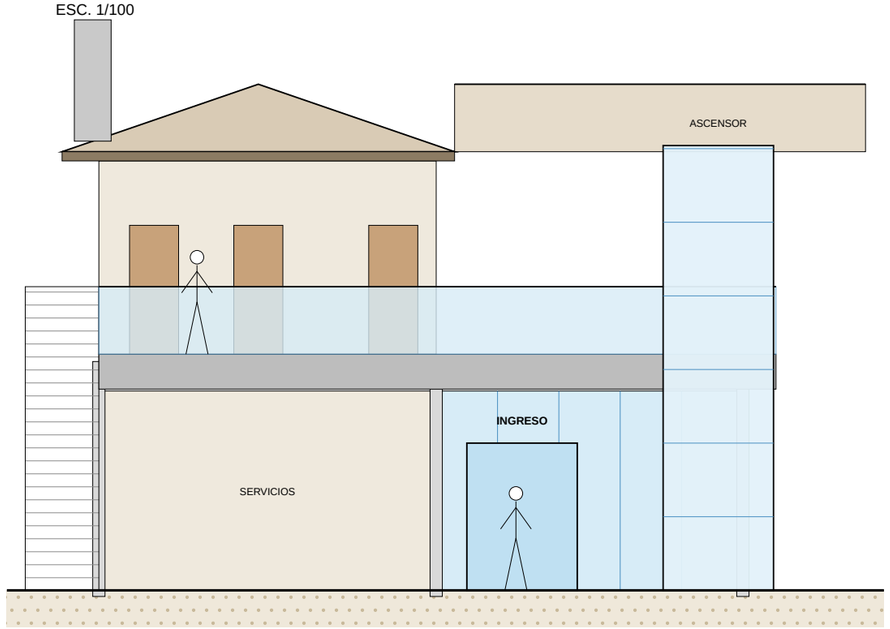


## ELEVACIÓN DE INGRESO (FACHADA ONO)

ESC. 1/100

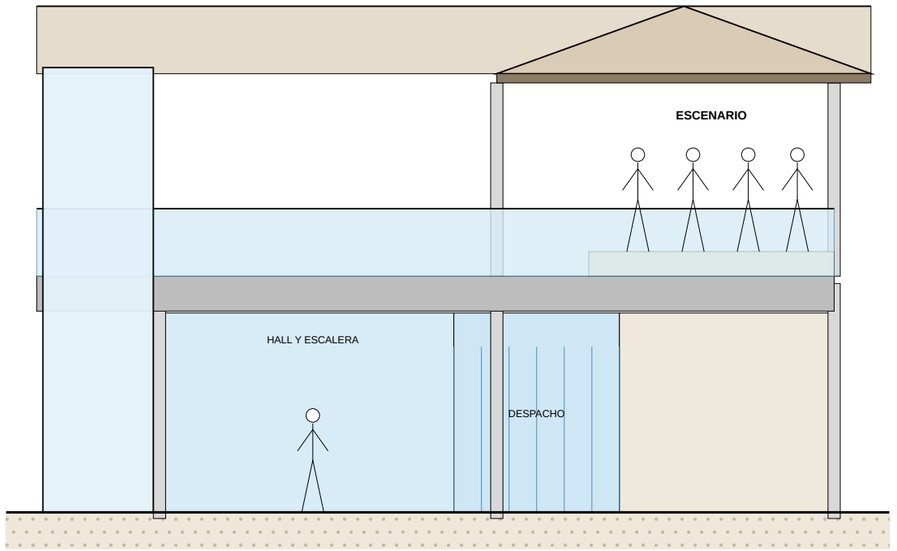


## ELEVACIÓN LATERAL (FACHADA SSO)

ESC. 1/100

| NIVELES Y ALTURAS | m |
|---|---|
| Nivel de piso terminado del 1.er piso | ±0.00 |
| Nivel de piso terminado del 2.º piso | +3.85 |
| Tarima del escenario | +4.25 |
| Altura libre bajo vigas (1.er piso) | 2.95 |
| Alero de los techos | +7.15 |
| Cumbrera de los techos | +8.25 |
| Remate de las chimeneas | +9.30 |
| Barandas de la terraza | 1.10 |

| ELEMENTO | ACABADO / MATERIAL |
|---|---|
| Estructura | Acero ASTM A572 / A500, pintura epóxica + esmalte |
| Entrepiso | Losa colaborante AD-600, e = 12 cm |
| Techos | Panel sándwich termoacústico, color teja |
| Fachadas 1.er piso | Ladrillo tarrajeado y mamparas de vidrio |
| Fachadas 2.º piso | Fibrocemento con listones de madera |
| Barandas | Vidrio laminado 10 mm + pasamanos inox. |
| Porches y terraza | Piedra o laja / porcelanato exterior |

## NOTAS

1. Cortes según las marcas X-X e Y-Y de las láminas A-05 y A-06.
2. Pórticos arriostrados en X en ambos sentidos (ver E-02); columnas HSS 8x8 desde la zapata hasta el alero.
3. Las chimeneas de los hornos atraviesan el bar en un ducto cortafuego y rematan 1.00 m sobre la cumbrera.
4. Techos a dos aguas con pendiente de 34 % (bar) y 36 % (escenario), canaletas y bajadas a jardines.

PROYECTO

**POLLERÍA CAMPESTRE**

ANTEPROYECTO - EDIFICIO DE ESTRUCTURA METÁLICA

UBICACIÓN

Jr. Rodríguez de Mendoza esq. calle lateral
Dist. San Nicolás (Mendoza) - Prov. Rodríguez de Mendoza
Departamento de Amazonas - Perú

PROPIETARIO

_____

PROFESIONAL RESPONSABLE (FIRMA Y SELLO)

Arq. / Ing. CIP N.° _____

PLANO

**CORTES Y ELEVACIONES**

EDIFICIO CENTRAL DE ESTRUCTURA METÁLICA

| ESCALA | FECHA |
|---|---|
| 1/100 | NOVIEMBRE 2026 |


ESPECIALIDAD

**ARQUITECTURA**

LÁMINA


**A-07**

7 de 10

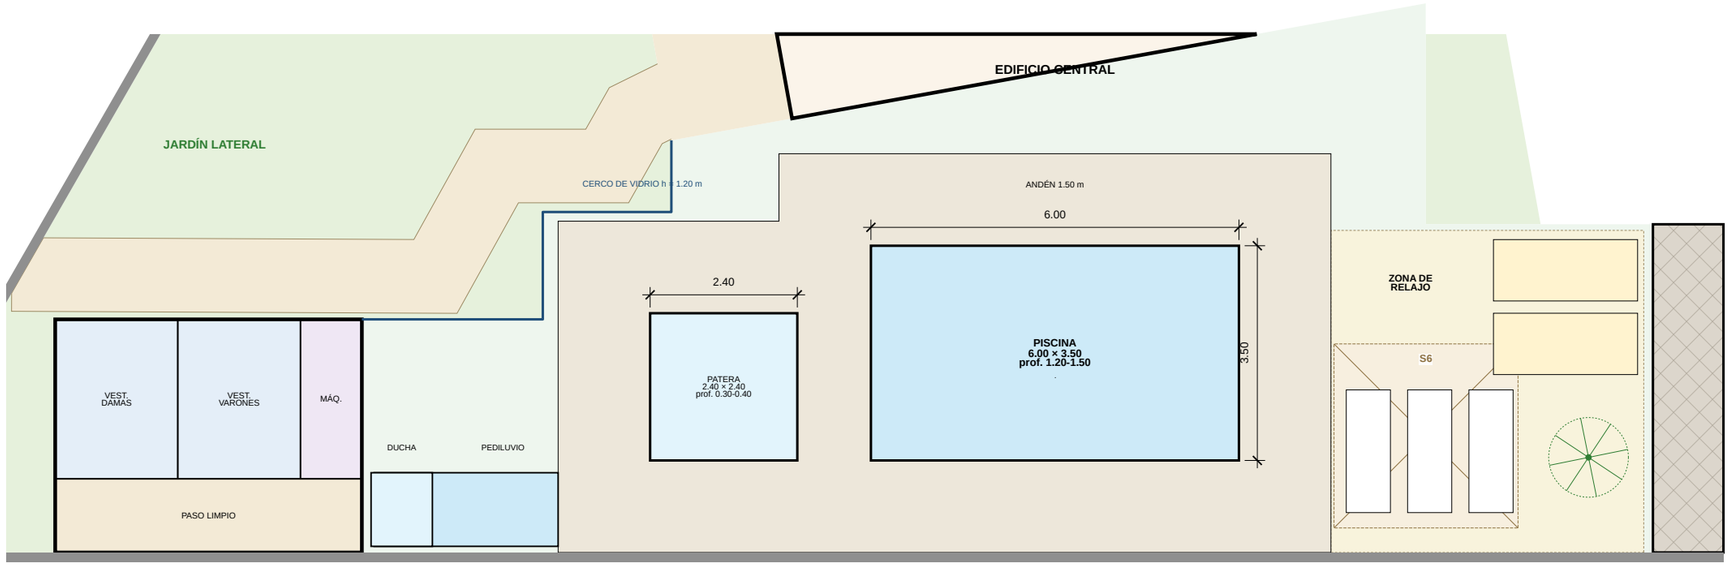



## PLANTA DE LA ZONA DE PISCINA

ESC. 1/100

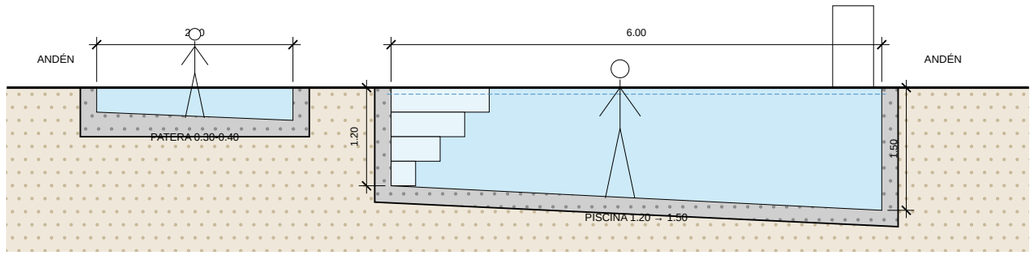


## CORTE LONGITUDINAL: PATERA Y PISCINA

ESC. 1/75

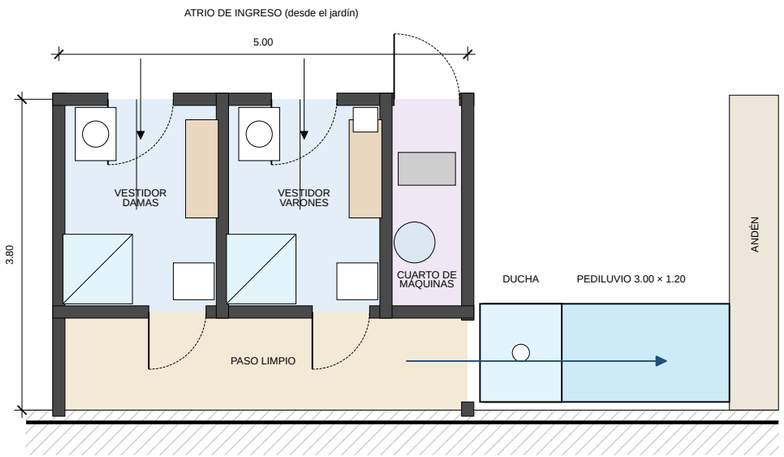


## VESTIDORES, DUCHA Y PEDILUVIO

ESC. 1/75

| DATOS DE LA PISCINA | |
|---|---|
| Piscina de adultos (6.00 × 3.50 m) | 21.0 m² |
| Patera para niños (2.40 × 2.40 m) | 5.8 m² |
| Volumen de agua total | 30.4 m³ |
| Recirculación mínima (3 veces/día) | 3.8 m³/h |
| Aforo de bañistas (2.0 m²/bañista) | 13 pers. |
| Andén perimetral | 1.50 m |
| Vestidores damas / varones | 5.2 / 5.2 m² |
| Pediluvio | 3.00 × 1.20 m |
| Zona de relajo | 26.8 m² |

## NOTAS

1. Recorrido obligatorio: atrio → vestidor → paso limpio → ducha → pediluvio → andén (D.S. 007-2003-SA y R.M. 213-2024 de la DIGESA, a confirmar).
2. Cerco de vidrio templado de 1.20 m con puerta de cierre automático; la patera queda separada del vaso de adultos.
3. Pisos antideslizantes, bordes redondeados, profundidades rotuladas en el borde y escalerilla de acero inoxidable.
4. Equipo: filtro de arena, bomba, clorador y tablero en el cuarto de máquinas (acceso desde el jardín); cloro libre 0.4-1.0 ppm, pH 7.2-7.8.
5. Salvavidas o vigilante durante el horario de uso, botiquín y teléfono; autorización sanitaria de la DIRESA Amazonas antes de abrir.
6. Zona de relajo: 3 camillas, 2 hamacas y la sombrilla S6 trasladada del jardín posterior.

PROYECTO

**POLLERÍA CAMPESTRE**

ANTEPROYECTO - EDIFICIO DE ESTRUCTURA METÁLICA

UBICACIÓN

Jr. Rodríguez de Mendoza esq. calle lateral
Dist. San Nicolás (Mendoza) - Prov. Rodríguez de Mendoza
Departamento de Amazonas - Perú

PROPIETARIO

_____

PROFESIONAL RESPONSABLE (FIRMA Y SELLO)

Arq. / Ing. CIP N.° _____


PLANO

**PISCINA, VESTIDORES Y RELAJO**

2.ª ETAPA (D.S. 007-2003-SA)

| ESCALA | FECHA |
|---|---|
| **INDICADA** | **NOVIEMBRE 2026** |

| ESPECIALIDAD | LÁMINA |
|---|---|
| **ARQUITECTURA** | **A-08** 8 de 10 |

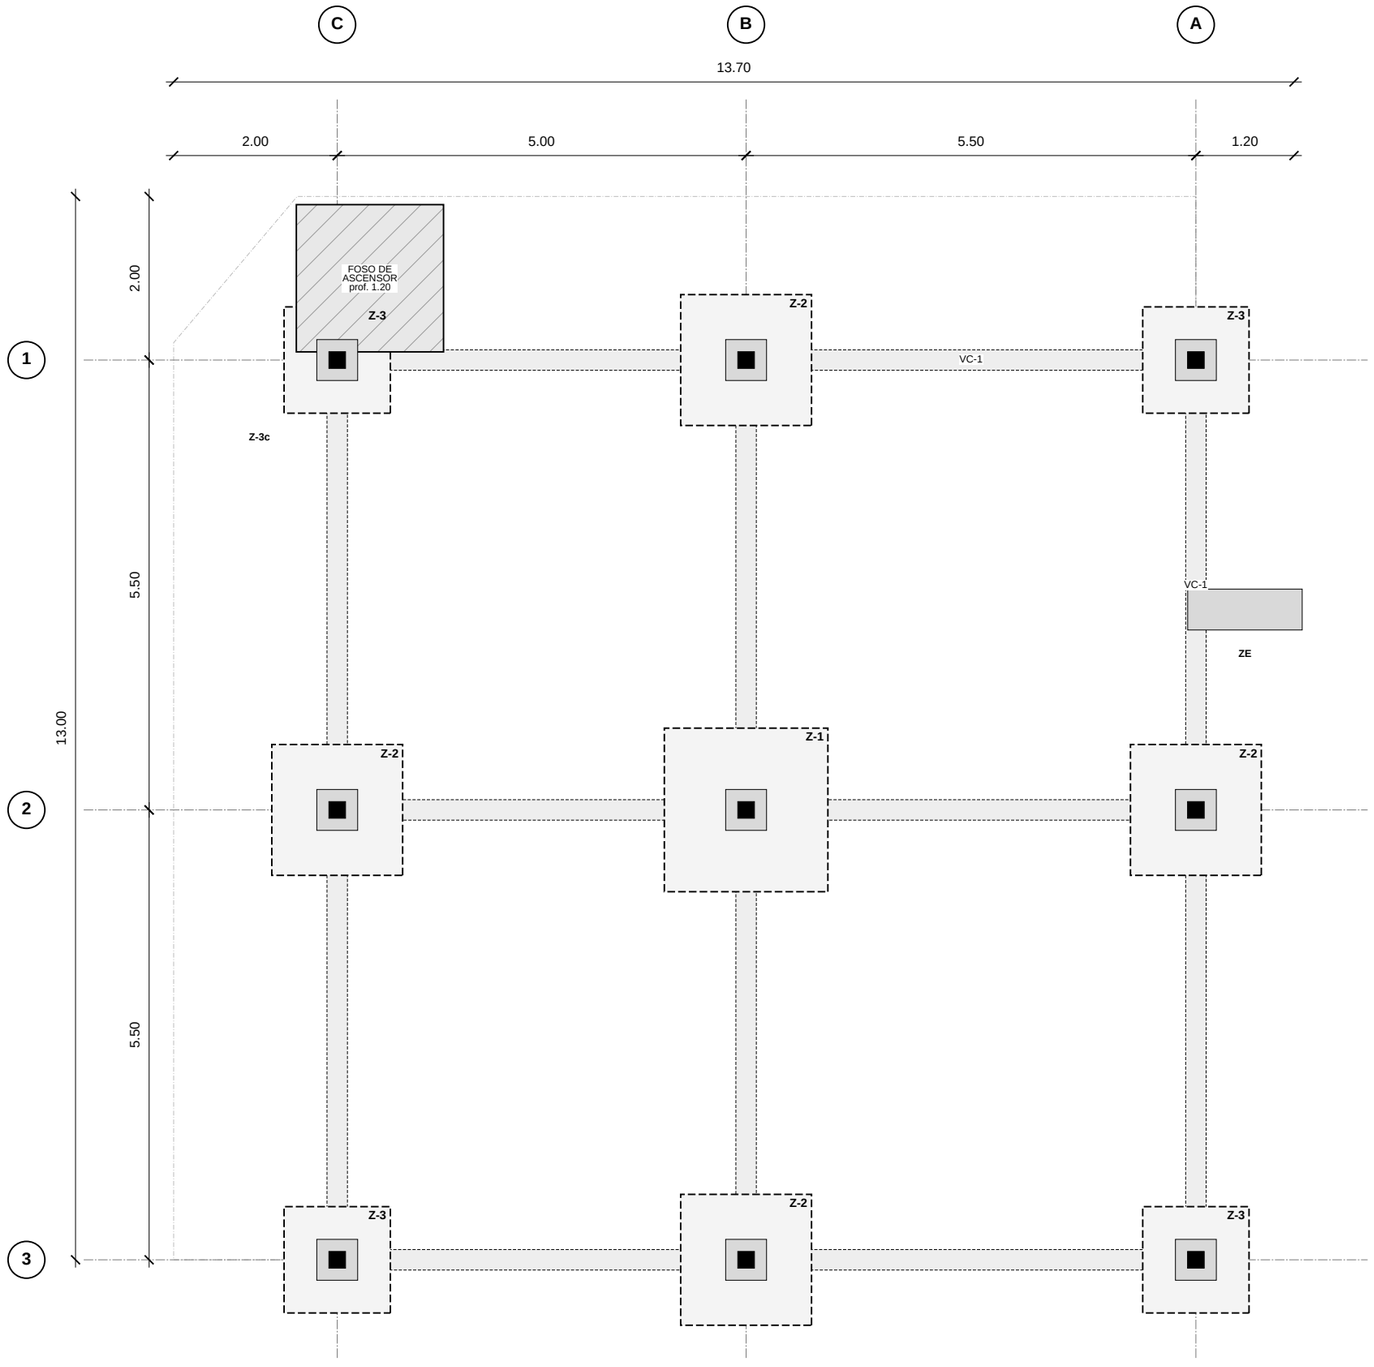



## PLANTA DE CIMENTACIÓN

ESC. 1/75

0 1 2 3 4 5 m

## DETALLE TÍPICO DE ZAPATA Z-1

ESC. 1/40

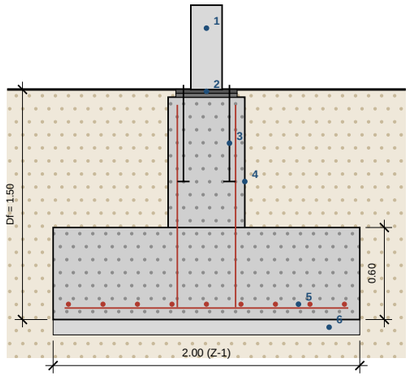


1. Columna HSS 8x8x1/4
2. PL 400×400×25 + grout 25 mm
3. 4 pernos Ø 3/4" L = 0.60 m
4. Pedestal 0.50×0.50, 8 Ø 5/8"
5. Malla Ø 5/8" @ 0.20 (2 direcc.)
6. Solado e = 0.10 m

N

## CUADRO DE ZAPATAS

| COD. | TIPO | B × L (m) | h (m) | P (kN) | CANT. |
|---|---|---|---|---|---|
| Z-1 | interior | 2.00 × 2.00 | 0.60 | 358 | 1 |
| Z-2 | borde | 1.60 × 1.60 | 0.50 | 231 | 4 |
| Z-3 | esquina | 1.30 × 1.30 | 0.50 | 139 | 4 |

| ESPECIFICACIÓN | VALOR |
|---|---|
| Concreto zapatas, pedestales, VC | f'c = 210 kg/cm² |
| Solado | f'c = 100 kg/cm², e = 0.10 m |
| Acero de refuerzo | fy = 4 200 kg/cm² (ASTM A615 G60) |
| Recubrimiento zapatas / VC | 7.5 cm / 4.0 cm |
| Viga de cimentación VC-1 | 0.25 × 0.40, 4 Ø 5/8", est. Ø 3/8" |
| Pernos de anclaje | ASTM F1554 Gr. 36, Ø 3/4", L = 0.60 m |
| Capacidad portante (supuesta) | q adm = 1.0 kg/cm² |

## NOTAS

1. Predimensionamiento de anteproyecto (E.020, E.030, E.050, E.060, E.090). Antes de construir: estudio de mecánica de suelos (EMS) y cálculo estructural firmado por ingeniero civil colegiado.
2. Si el EMS da una capacidad menor o suelos expansivos, recalcular las zapatas o usar platea.
3. ZE: zapata de apoyo de la escalera exterior (0.50 × 1.40 × 0.40 m); la escalera principal se apoya en la viga VC-1 del eje 1. Z-3c: zapata del eje C-1 combinada con el foso del ascensor (según el proveedor).
4. Cotas de las zapatas centradas en los ejes; nivel de fondo -1.50 m respecto del NPT ±0.00.

PROYECTO

**POLLERÍA CAMPESTRE**

ANTEPROYECTO - EDIFICIO DE ESTRUCTURA METÁLICA

UBICACIÓN

Jr. Rodríguez de Mendoza esq. calle lateral
Dist. San Nicolás (Mendoza) - Prov. Rodríguez de Mendoza
Departamento de Amazonas - Perú

PROPIETARIO

_____

PROFESIONAL RESPONSABLE (FIRMA Y SELLO)

Arq. / Ing. CIP N.° _____


PLANO

**CIMENTACIÓN**

ZAPATAS, PEDESTALES Y VIGAS DE CIMENTACIÓN

| ESCALA | FECHA |
|---|---|
| INDICADA | NOVIEMBRE 2026 |


| ESPECIALIDAD | LÁMINA |
|---|---|
| ESTRUCTURAS | E-01 |
| | 9 de 10 |

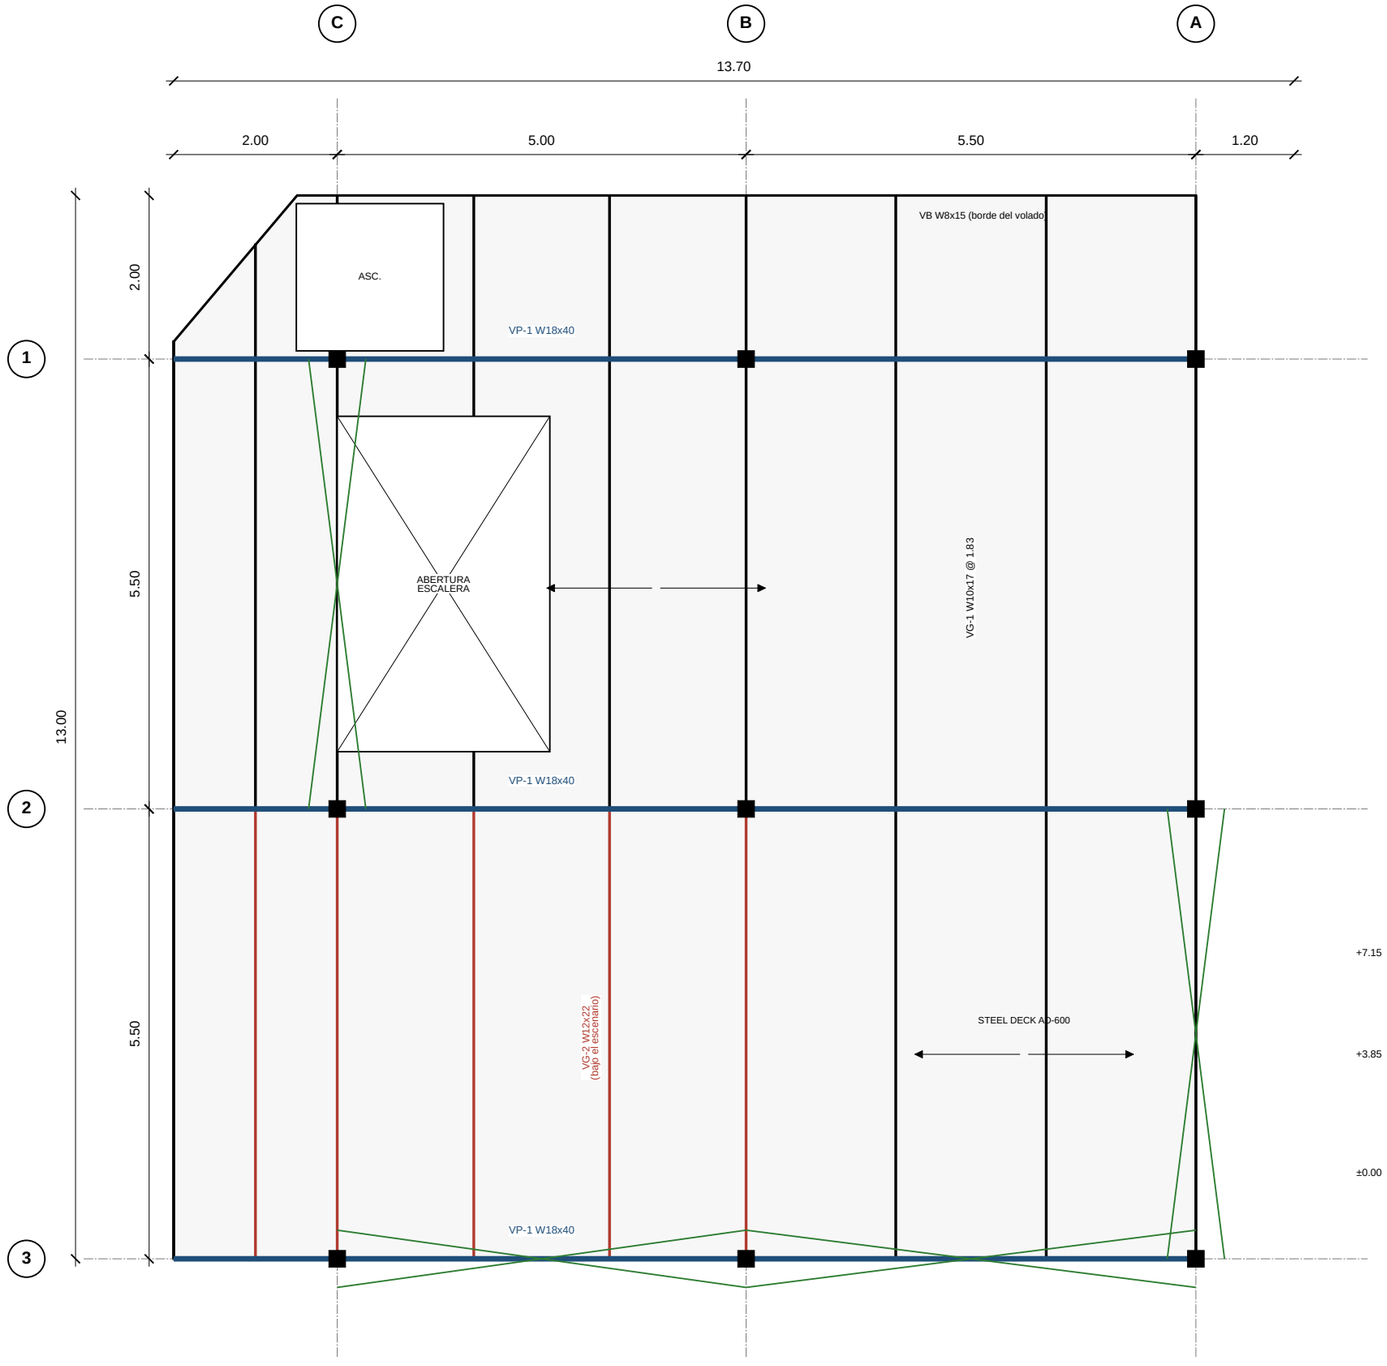


## PLANTA DE ENTREPISO +3.85

ESC. 1/75

0 1 2 3 4 5 m

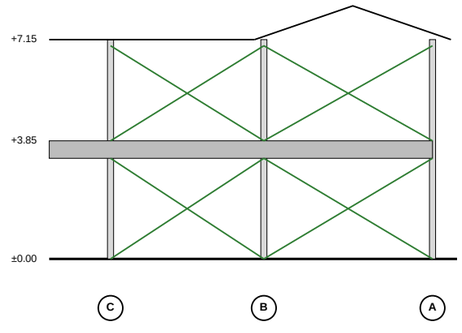


## PÓRTICO ARRIOSTRADO - EJE 3

ESC. 1/200

N

## CUADRO DE SECCIONES

| ELEMENTO | SECCIÓN | MATERIAL |
|---|---|---|
| Columnas | HSS 8x8x1/4 | ASTM A500 Gr. C |
| VP-1 vigas principales | W18x40 | ASTM A572 Gr. 50 |
| VG-1 viguetas | W10x17 | ASTM A572 Gr. 50 |
| VG-2 viguetas (escenario) | W12x22 | ASTM A572 Gr. 50 |
| VB vigas de borde | W8x15 | ASTM A572 Gr. 50 |
| Arriostres en X | HSS 4x4x1/4 | ASTM A500 Gr. C |
| Vigas de techo | W8x13 | ASTM A572 Gr. 50 |
| Correas | C 150×50×15×2.5 | ASTM A653 |
| Losa | AD-600 + 12 cm | f'c 210 kg/cm² |

## PREDIMENSIONAMIENTO (LRFD)

Losa colaborante: Steel deck AD-600 cal. 20 + concreto f'c 210 kg/cm², e = 12 cm; luz 1.83 m

Viguetas: W10x17 @ 1.83 m, L = 5.50 m (uso 82 %, flecha 13 mm ≤ 15); bajo el escenario W12x22

Vigas principales: W18x40, L = 5.50 m + volado 2.00 m (uso 89 %)

Columnas: HSS 8x8x1/4, Pu = 518 kN, φPn = 1118 kN, interacción 0.76

Arriostres: HSS 4x4x1/4 en X, F = 63 kN, φPn = 373 kN

Sismo: Z 0.35 · U 1.3 · C 2.5 · S 1.15 / R 7 = 0.187; P = 996 kN; V = 186 kN

Zapatas: interior 2.0 × 2.0 m, borde 1.6 m, esquina 1.3 m; q adm supuesta 1.0 kg/cm²

Acero estructural: 14,979 kg (93 kg por m² de entrepiso)

## NOTAS

1. Cargas: muerta de losa 3.55 kPa + tabiquería 0.5 kPa; viva de terraza 4.0 kPa y de escenario 7.5 kPa (E.020), esta última en vigas, columnas y zapatas.
2. Sismo (E.030): sistema de pórticos arriostrados concéntricos (R = 7), del lado seguro con Z = 0.35 y U = 1.3 hasta confirmar la zonificación vigente.
3. Conexiones atornilladas ASTM A325 y soldadura E70XX; pintura epóxica de 2 capas y esmalte de acabado.
4. Arriostres en planta (verde): eje 3 (A-B y B-C), eje A (2-3) y eje C (1-2) en el 1.er piso; en el 2.º piso el del eje A pasa al paño 1-2.

PROYECTO

**POLLERÍA CAMPESTRE**

ANTEPROYECTO - EDIFICIO DE ESTRUCTURA METÁLICA

UBICACIÓN

Jr. Rodríguez de Mendoza esq. calle lateral
Dist. San Nicolás (Mendoza) - Prov. Rodríguez de Mendoza
Departamento de Amazonas - Perú

PROPIETARIO

_____

PROFESIONAL RESPONSABLE (FIRMA Y SELLO)

Arq. / Ing. CIP N.° _____

PLANO

**ESTRUCTURA METÁLICA**

ENTREPISO +3.85, ARRIOSTRES Y PÓRTICO DEL EJE 3

| ESCALA | FECHA |
|---|---|
| **INDICADA** | **NOVIEMBRE 2026** |

| ESPECIALIDAD | LÁMINA |
|---|---|
| **ESTRUCTURAS** | **E-02** 10 de 10 |