

PLANIMETRÍA GENERAL - 1.ª ETAPA

ESC. 1/150

0 2 4 6 8 10 m

CUADRO DE ÁREAS	m²
Área del terreno	820.2
Almacén de leña y garaje (existentes)	75.7
Calzada, estacionamientos, motos y GLP	215.8
Edificio: 1.er piso cerrado	115.5
Porches techados (bajo el 2.º piso)	45.7
Veredas, caminos y escalera exterior	43.0
Jardines y setos	306.7
2.º piso: bar, SS.HH., terraza y escenario (techado parcial)	161.2

Área techada total (1.er + 2.º piso): 276.7 m²

CAPACIDAD (MODO RESTAURANTE)	MESAS	ASIENTOS
Jardines: sombrillas (mesas de 6 y 4)	10	58
1.er piso: despacho y porches (mesas de 2 y 4)	7	24
2.º piso: terraza (mesas de 4) y barras	6	31
TOTAL MODO RESTAURANTE		**113**

LEYENDA

- Jardín (césped)
- Seto vivo tras el cerco de los frentes
- Caminos, vereda y porches (piedra o laja)
- Calzada y estacionamientos (adoquín de concreto)
- Estructuras existentes que se conservan
- Sombrilla profesional 3.00 × 3.00 m (removible)
- Árbol / palmera
- Proyección del 2.º piso (volados de 2.00 m)
- Columna metálica HSS 8x8x1/4

NOTAS

1. Cotas en metros. Las estructuras de leña y garaje existentes se conservan; el garaje se usa por la misma calzada.
2. Las sombrillas S1 a S10 se anclan en camisas metálicas empotradas al ras del césped: se retiran en minutos para eventos (ver A-04).
3. El jardín posterior (S6 a S10) se reserva para la piscina de la 2.ª etapa (ver A-02).
4. Estacionamiento descubierto: 5 plazas (1 accesible 3.80 × 5.00 m) + 2 motos. Para eventos se coordina estacionamiento en la vía (ver A-03).

VANO	DESCRIPCIÓN	ANCHO
V-1	Portón de 2 hojas batientes (madera y acero)	6.00
P-1	Portada principal de 2 hojas con techo de teja	3.00
P-2	Puerta de servicio y evacuación del 2.º piso	1.80
P-3	Salida de emergencia, barra antipánico	1.20
P-4	Puerta de la caseta de GLP y residuos	1.60

PROYECTO

POLLERÍA CAMPESTRE

ANTEPROYECTO - EDIFICIO DE ESTRUCTURA METÁLICA

UBICACIÓN

Jr. Rodríguez de Mendoza esq. calle lateral
Dist. San Nicolás (Mendoza) - Prov. Rodríguez de Mendoza
Departamento de Amazonas - Perú

PROPIETARIO

_____

PROFESIONAL RESPONSABLE (FIRMA Y SELLO)

Arq. / Ing. CIP N.° _____

PLANO

PLANIMETRÍA GENERAL

1.ª ETAPA: RESTAURANTE Y JARDINES

ESCALA	FECHA
1/150	NOVIEMBRE 2026

ESPECIALIDAD

ARQUITECTURA

LÁMINA

A-01

1 de 10



PLANIMETRÍA GENERAL - 2.ª ETAPA

ESC. 1/150

0 2 4 6 8 10 m

CUADRO DE ÁREAS	m²
Área del terreno	820.2
Almacén de leña y garaje (existentes)	75.7
Calzada, estacionamientos, motos y GLP	215.8
Edificio: 1.er piso cerrado	115.5
Porches techados (bajo el 2.º piso)	45.7
Veredas, caminos y escalera exterior	43.0
Piscina, andenes, vestidores y relajo	158.0
Jardines y setos	148.7
2.º piso: bar, SS.HH., terraza y escenario (techado parcial)	161.2

Área techada total (1.er + 2.º piso): 276.7 m²

CAPACIDAD (MODO RESTAURANTE)	MESAS	ASIENTOS
Jardines: sombrillas (mesas de 6 y 4)	5	28
Zona de relajo: camillas y hamacas	5	-
1.er piso: despacho y porches (mesas de 2 y 4)	7	24
2.º piso: terraza (mesas de 4) y barras	6	31
TOTAL MODO RESTAURANTE		**83**

LEYENDA

- Jardín (césped)
- Seto vivo tras el cerco de los frentes
- Caminos, vereda y porches (piedra o laja)
- Calzada y estacionamientos (adoquín de concreto)
- Piscina y patera (2.ª etapa)
- Estructuras existentes que se conservan
- Sombrilla profesional 3.00 × 3.00 m (removible)
- Árbol / palmera
- Proyección del 2.º piso (volados de 2.00 m)
- Columna metálica HSS 8x8x1/4

NOTAS

1. La piscina se separa del jardín con cerco de vidrio templado de 1.20 m; se entra solo por los vestidores, ducha y pediluvio (D.S. 007-2003-SA).
2. En la 2.ª etapa la sombrilla S6 pasa a la zona de relajo; S7 a S10 se guardan para eventos o se reubican.
3. Requiere autorización sanitaria de la DIRESA Amazonas, salvavidas en horario de uso y señalización de profundidades.

VANO	DESCRIPCIÓN	ANCHO
V-1	Portón de 2 hojas batientes (madera y acero)	6.00
P-1	Portada principal de 2 hojas con techo de teja	3.00
P-2	Puerta de servicio y evacuación del 2.º piso	1.80
P-3	Salida de emergencia, barra antipánico	1.20
P-4	Puerta de la caseta de GLP y residuos	1.60

PROYECTO

POLLERÍA CAMPESTRE

ANTEPROYECTO - EDIFICIO DE ESTRUCTURA METÁLICA

UBICACIÓN

Jr. Rodríguez de Mendoza esq. calle lateral
Dist. San Nicolás (Mendoza) - Prov. Rodríguez de Mendoza
Departamento de Amazonas - Perú

PROPIETARIO

_____

PROFESIONAL RESPONSABLE (FIRMA Y SELLO)

Arq. / Ing. CIP N.° _____

PLANO

PLANIMETRÍA GENERAL

2.ª ETAPA: PISCINA, VESTIDORES Y RELAJO

ESCALA	FECHA
1/150	NOVIEMBRE 2026

ESPECIALIDAD

ARQUITECTURA

LÁMINA

A-02

2 de 10



CIRCULACIONES Y RUTAS DE EVACUACIÓN

ESC. 1/150

0 2 4 6 8 10 m

LEYENDA

- Circulación vehicular (doble sentido)
- Circulación peatonal del público
- Recorridos por jardines y caminos
- Servicio: personal y proveedores (P-2)
- Leña: del almacén existente a la cocina
- Ruta de evacuación hacia la salida

RUTA	RECORRIDO DE EVACUACIÓN	m
R1	Escenario → escalera exterior → vereda → P-2	36
R2	Terraza → escalera principal → hall → P-1	23
R3	Cocina → ingreso de servicio → vereda → P-2	19
R4	SS.HH. → despacho → porche lateral → P-3	24
R5	Garaje y estacionamientos → calzada → V-1	24

Recorrido máximo admisible hasta una salida: 45 m (A.130).

SALIDA / ESCALERA	ANCHO m	CAPAC. pers.
P-1	3.00	600
V-1	6.00	1 200
P-2	1.80	360
P-3	1.20	240
Escalera principal (2.º piso)	1.20	150
Escalera exterior (2.º piso)	1.20	150

Capacidad: puertas 0.005 m/pers.; escaleras 0.008 m/pers. (A.130).

NOTAS

1. La calzada de 6.00 m permite el cruce de dos vehículos y el acceso del camión de GLP y proveedores hasta la zona de carga.
2. Peatones y vehículos se separan: el público entra por P-1 (Jr. Rodríguez de Mendoza) y el servicio por P-2 (calle lateral).
3. En eventos: portón V-1 abierto y señalizado, personal de control en P-1 y luces de emergencia en caminos y escaleras.
4. Señalización de seguridad según NTP 399.010-1; extintores PQS en cada nivel y K en la cocina.

PROYECTO

POLLERÍA CAMPESTRE

ANTEPROYECTO - EDIFICIO DE ESTRUCTURA METÁLICA

UBICACIÓN

Jr. Rodríguez de Mendoza esq. calle lateral
Dist. San Nicolás (Mendoza) - Prov. Rodríguez de Mendoza
Departamento de Amazonas - Perú

PROPIETARIO

_____

PROFESIONAL RESPONSABLE (FIRMA Y SELLO)

Arq. / Ing. CIP N.° _____

PLANO

CIRCULACIONES Y EVACUACIÓN

VEHICULAR, PEATONAL, SERVICIO Y RUTAS DE ESCAPE

ESCALA	FECHA
1/150	NOVIEMBRE 2026

ESPECIALIDAD	LÁMINA
ARQUITECTURA	A-03
	3 de 10




MODO RESTAURANTE

ESC. 1/300



MODO EVENTO (SOMBRILLAS RETIRADAS)

ESC. 1/300

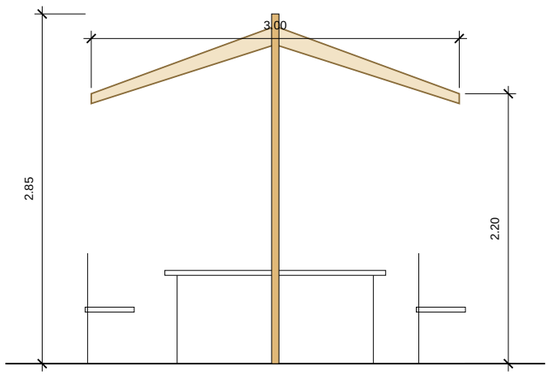


SOMBRILLA 3.00 × 3.00 m

ESC. 1/50

DETALLE: ANCLAJE REMOVIBLE

ESC. 1/20

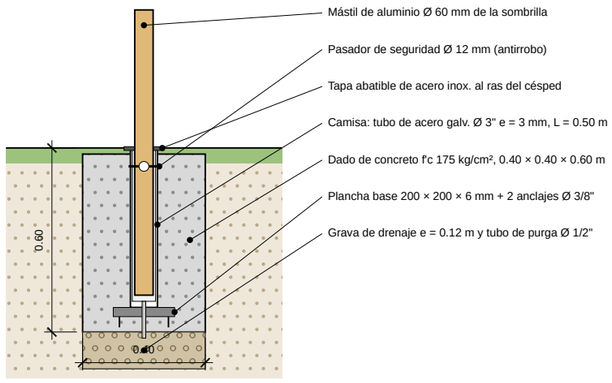

1.ª ETAPA	RESTAURANTE	EVENTO
Sombrillas 3.00 × 3.00 m instaladas	10	0
Asientos en jardines	58	96
Mesas en jardines	10 (de 6 y 4)	12 redondas de 8
Pista de baile	-	31.5 m²
Césped libre para el evento	-	307 m²
Aforo de pie en jardines (1.0 m²/pers.)	-	307 pers.

NOTAS

1. Cada sombrilla se ancla en una camisa empotrada en un dado de concreto bajo el césped; para un evento se retira el pasador, se levanta el mástil y se cierra la tapa al ras: el jardín queda libre en minutos y sin bases que estorben.
2. Las sombrillas retiradas se guardan cerradas en el depósito bajo la escalera o en el garaje; pueden reinstalarse en cualquier camisa o sobre bases móviles lastradas (4 × 25 kg) donde convenga.
3. Sombrilla profesional de mástil central de aluminio, lona acrílica 3.00 × 3.00 m resistente al agua y UV, con faldón; retirar o cerrar con viento > 40 km/h.
4. Modo evento: mesas redondas de 8 personas, pista de baile sobre el césped (tarima modular opcional), buffet bajo el porche lateral y la música en el escenario de la terraza.
5. En la 2.ª etapa el jardín posterior pasa a ser la zona de piscina; el modo evento usa el jardín de ingreso, el jardín lateral, los porches y la terraza.

PROYECTO

POLLERÍA CAMPESTRE

ANTEPROYECTO - EDIFICIO DE ESTRUCTURA METÁLICA

UBICACIÓN

Jr. Rodríguez de Mendoza esq. calle lateral
Dist. San Nicolás (Mendoza) - Prov. Rodríguez de Mendoza
Departamento de Amazonas - Perú

PROPIETARIO

_____

PROFESIONAL RESPONSABLE (FIRMA Y SELLO)

Arq. / Ing. CIP N.° _____

PLANO

SOMBRILLAS REMOVIBLES

MODO RESTAURANTE / MODO EVENTO Y ANCLAJE

ESCALA	FECHA
INDICADA	**NOVIEMBRE 2026**

ESPECIALIDAD	LÁMINA
ARQUITECTURA	**A-04** 4 de 10



PLANTA DEL 1.er PISO

ESC. 1/75

N

AMBIENTE	m²
SS.HH. y vestidor del personal	2.9
Almacén de insumos	4.3
Ingreso de servicio	6.6
Cocina: horno pollero, parrilla y freidoras	27.5
Lavado de vajilla	7.0
Preparación fría y maceración	6.3
Cámara y bebidas	5.9
Hall de ingreso	11.5
Escalera principal	11.4
Ascensor	3.2
Despacho, caja y mesas	13.5
Lavatorios	6.0
SS.HH. accesible	4.8
SS.HH. damas	3.5
SS.HH. varones	3.2
Porches techados (bajo el 2.º piso)	42.4

CÓD.	EQUIPAMIENTO DE COCINA
HP-1, HP-2	Hornos polleros a leña, 40 pollos c/u, con chimenea
PA	Parrilla a carbón 1.10 × 0.90 m
FR	Freidoras a gas (2), con extintor clase K
MT	Mesa de trabajo de acero inox. (isla)
PC	Pase caliente y despacho a la caja
LV / MM	Lavadero de 2 pozas / mesa de maceración
CF / DC	Conservadoras y cámara / mostrador y caja

NOTAS

1. Línea de fuego contra el muro de servicio bajo campana de 5.00 m (filtros, ducto y extractor); hornos con chimenea propia hasta 1.00 m sobre la cumbrera.
2. Cocina: piso antideslizante con sumidero y trampa de grasas; muros con enchape hasta 2.10 m; extintor clase K a menos de 9 m de las freidoras y extintor de agua para los hornos a leña.
3. El ascensor panorámico (cabina 1.20 × 1.40 m) y el SS.HH. accesible cumplen la Norma A.120.
4. La leña llega por la calzada desde el almacén existente hasta el ingreso de servicio.

PROYECTO

POLLERÍA CAMPESTRE

ANTEPROYECTO - EDIFICIO DE ESTRUCTURA METÁLICA

UBICACIÓN

Jr. Rodríguez de Mendoza esq. calle lateral
Dist. San Nicolás (Mendoza) - Prov. Rodríguez de Mendoza
Departamento de Amazonas - Perú

PROPIETARIO

_____

PROFESIONAL RESPONSABLE (FIRMA Y SELLO)

Arq. / Ing. CIP N.° _____

PLANO

PLANTA DEL 1.er PISO

COCINA, HORNOS, PARRILLA Y DESPACHO

ESCALA	FECHA
1/75	NOVIEMBRE 2026

ESPECIALIDAD

ARQUITECTURA

LÁMINA

A-05

5 de 10



PLANTA DEL 2.º PISO

ESC. 1/75

0 1 2 3 4 5 m

N

AMBIENTE	m²
SS.HH. accesible	5.0
SS.HH. damas	4.5
SS.HH. varones	4.2
Bar y bebidas	27.5
Depósito del bar	12.7
Pasillo de servicio y evacuación	6.6
Escenario (+0.40)	24.0
Terraza exterior	62.0
Escalera principal	11.4
Ascensor	3.2

AFORO DEL 2.° PISO (A.070)	m²	PERS.
Terraza: restaurante (1.5 m²/pers)	62	41
Terraza: evento, de pie (1.0 m²/pers)	62	62
Bar: zona de clientes (1.0 m²/pers)	9.7	10
Escenario: grupo musical	24	6-8

NOTAS

1. Escenario de 4.00 × 6.00 m sobre tarima modular de +0.40 m; la losa se diseña para 750 kgf/m² (E.020) y puede ampliarse con módulos sobre la terraza.
2. Dos rutas de evacuación: escalera principal en U (1.20 m) y escalera exterior de 1.20 m por el pasillo de servicio; esta última sirve también para subir los equipos de sonido.
3. Barandas de vidrio laminado de 1.10 m con pasamanos de acero inoxidable.
4. Muro acústico tras el escenario y techos con aislamiento termoacústico; espectáculos hasta las 22:00 o con estudio acústico (ECA ruido).
5. Líneas grises discontinuas: proyección de los techos a dos aguas del bar y del escenario.

PROYECTO

POLLERÍA CAMPESTRE

ANTEPROYECTO - EDIFICIO DE ESTRUCTURA METÁLICA

UBICACIÓN

Jr. Rodríguez de Mendoza esq. calle lateral
Dist. San Nicolás (Mendoza) - Prov. Rodríguez de Mendoza
Departamento de Amazonas - Perú

PROPIETARIO

_____

PROFESIONAL RESPONSABLE (FIRMA Y SELLO)

Arq. / Ing. CIP N.° _____


PLANO

PLANTA DEL 2.º PISO

BAR, TERRAZA Y ESCENARIO


ESCALA	FECHA
1/75	NOVIEMBRE 2026

ESPECIALIDAD	LÁMINA
ARQUITECTURA	A-06
	6 de 10

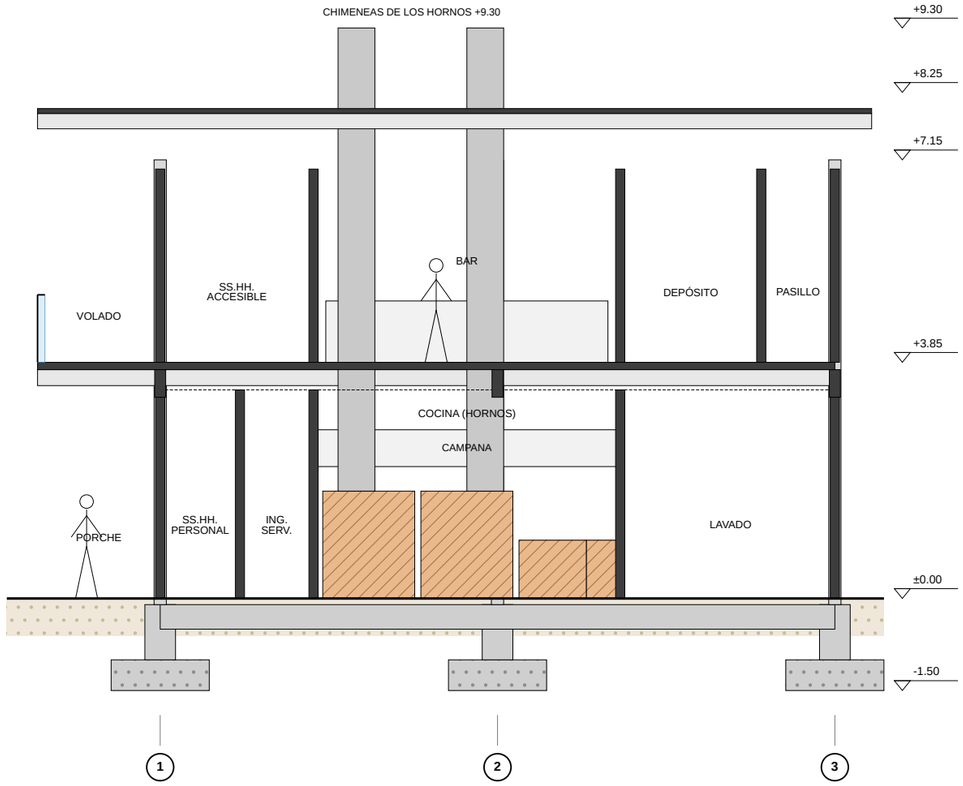


CORTE X-X

ESC. 1/100

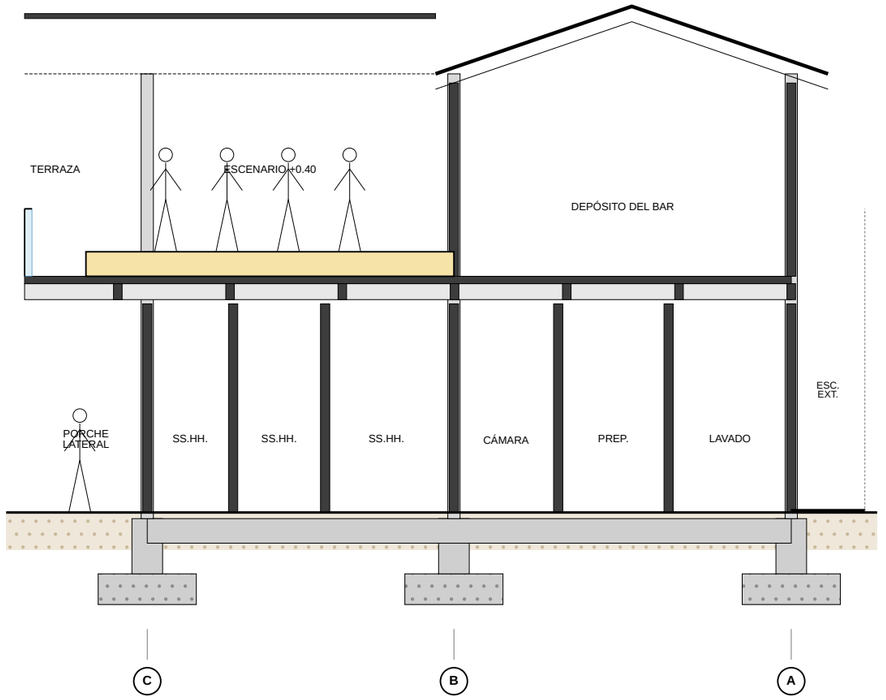


CORTE Y-Y

ESC. 1/100

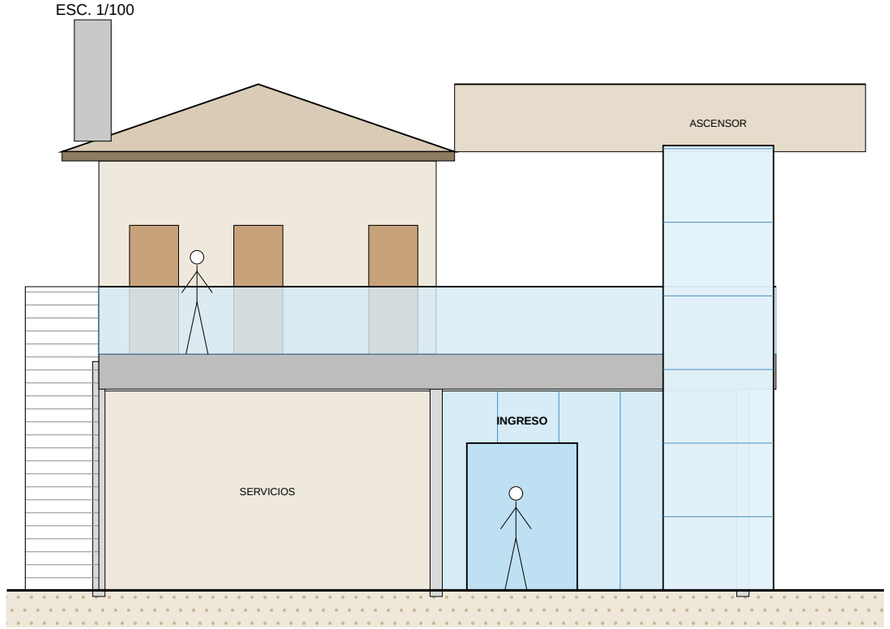

ELEVACIÓN DE INGRESO (FACHADA ONO)

ESC. 1/100

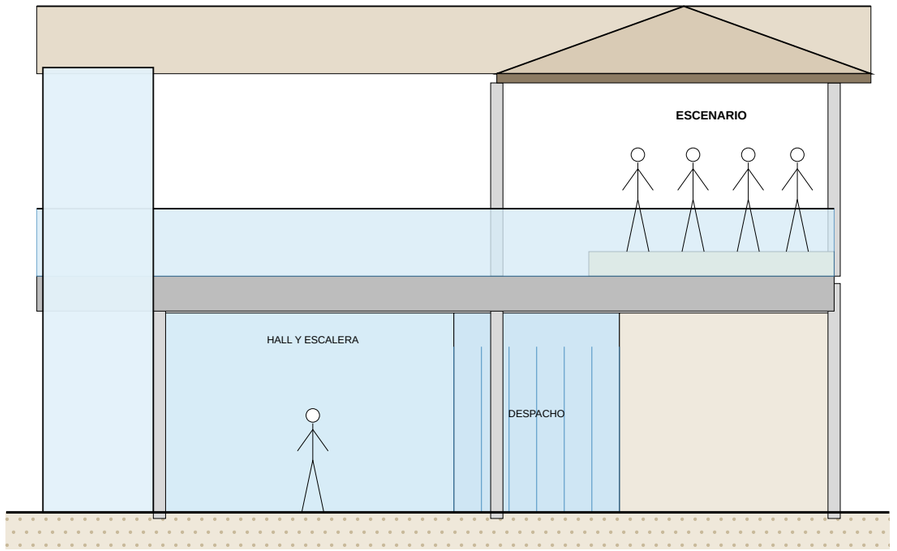

ELEVACIÓN LATERAL (FACHADA SSO)

ESC. 1/100

NIVELES Y ALTURAS	m
Nivel de piso terminado del 1.er piso	±0.00
Nivel de piso terminado del 2.º piso	+3.85
Tarima del escenario	+4.25
Altura libre bajo vigas (1.er piso)	2.95
Alero de los techos	+7.15
Cumbrera de los techos	+8.25
Remate de las chimeneas	+9.30
Barandas de la terraza	1.10

ELEMENTO	ACABADO / MATERIAL
Estructura	Acero ASTM A572 / A500, pintura epóxica + esmalte
Entrepiso	Losa colaborante AD-600, e = 12 cm
Techos	Panel sándwich termoacústico, color teja
Fachadas 1.er piso	Ladrillo tarrajeado y mamparas de vidrio
Fachadas 2.º piso	Fibrocemento con listones de madera
Barandas	Vidrio laminado 10 mm + pasamanos inox.
Porches y terraza	Piedra o laja / porcelanato exterior

NOTAS

1. Cortes según las marcas X-X e Y-Y de las láminas A-05 y A-06.
2. Pórticos arriostrados en X en ambos sentidos (ver E-02); columnas HSS 8x8 desde la zapata hasta el alero.
3. Las chimeneas de los hornos atraviesan el bar en un ducto cortafuego y rematan 1.00 m sobre la cumbrera.
4. Techos a dos aguas con pendiente de 34 % (bar) y 36 % (escenario), canaletas y bajadas a jardines.

PROYECTO

POLLERÍA CAMPESTRE

ANTEPROYECTO - EDIFICIO DE ESTRUCTURA METÁLICA

UBICACIÓN

Jr. Rodríguez de Mendoza esq. calle lateral
Dist. San Nicolás (Mendoza) - Prov. Rodríguez de Mendoza
Departamento de Amazonas - Perú

PROPIETARIO

_____

PROFESIONAL RESPONSABLE (FIRMA Y SELLO)

Arq. / Ing. CIP N.° _____

PLANO

CORTES Y ELEVACIONES

EDIFICIO CENTRAL DE ESTRUCTURA METÁLICA

ESCALA	FECHA
1/100	NOVIEMBRE 2026


ESPECIALIDAD

ARQUITECTURA

LÁMINA


A-07

7 de 10

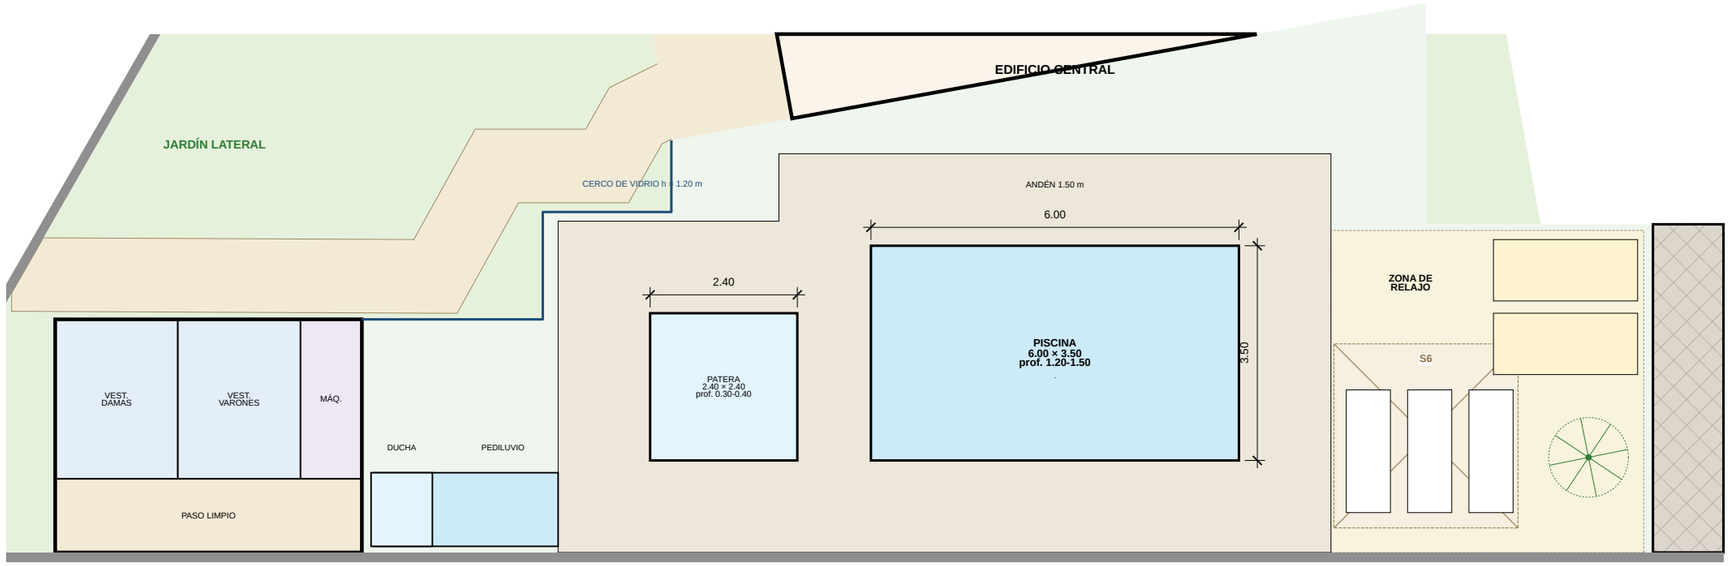


PLANTA DE LA ZONA DE PISCINA

ESC. 1/100

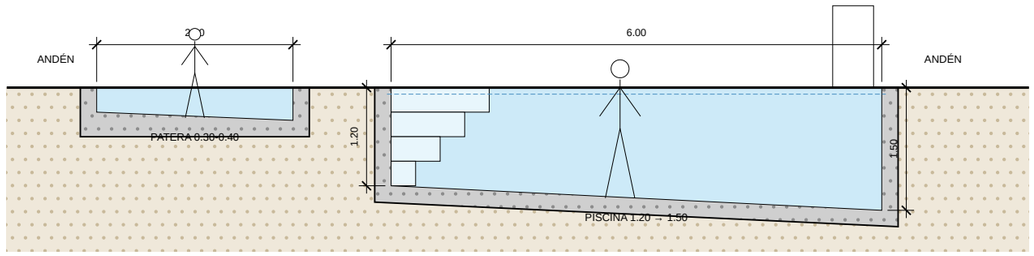

CORTE LONGITUDINAL: PATERA Y PISCINA

ESC. 1/75

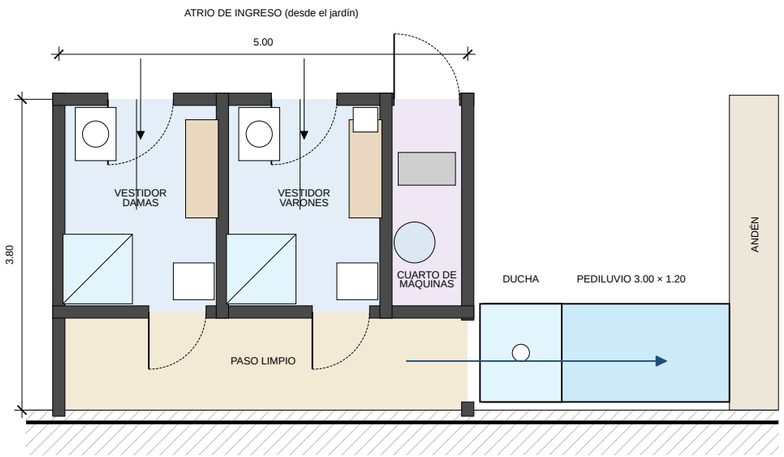

VESTIDORES, DUCHA Y PEDILUVIO

ESC. 1/75

DATOS DE LA PISCINA	
Piscina de adultos (6.00 × 3.50 m)	21.0 m²
Patera para niños (2.40 × 2.40 m)	5.8 m²
Volumen de agua total	30.4 m³
Recirculación mínima (3 veces/día)	3.8 m³/h
Aforo de bañistas (2.0 m²/bañista)	13 pers.
Andén perimetral	1.50 m
Vestidores damas / varones	5.2 / 5.2 m²
Pediluvio	3.00 × 1.20 m
Zona de relajo	26.8 m²

NOTAS

1. Recorrido obligatorio: atrio → vestidor → paso limpio → ducha → pediluvio → andén (D.S. 007-2003-SA y R.M. 213-2024 de la DIGESA, a confirmar).
2. Cerco de vidrio templado de 1.20 m con puerta de cierre automático; la patera queda separada del vaso de adultos.
3. Pisos antideslizantes, bordes redondeados, profundidades rotuladas en el borde y escalerilla de acero inoxidable.
4. Equipo: filtro de arena, bomba, clorador y tablero en el cuarto de máquinas (acceso desde el jardín); cloro libre 0.4-1.0 ppm, pH 7.2-7.8.
5. Salvavidas o vigilante durante el horario de uso, botiquín y teléfono; autorización sanitaria de la DIRESA Amazonas antes de abrir.
6. Zona de relajo: 3 camillas, 2 hamacas y la sombrilla S6 trasladada del jardín posterior.

PROYECTO

POLLERÍA CAMPESTRE

ANTEPROYECTO - EDIFICIO DE ESTRUCTURA METÁLICA

UBICACIÓN

Jr. Rodríguez de Mendoza esq. calle lateral
Dist. San Nicolás (Mendoza) - Prov. Rodríguez de Mendoza
Departamento de Amazonas - Perú

PROPIETARIO

_____

PROFESIONAL RESPONSABLE (FIRMA Y SELLO)

Arq. / Ing. CIP N.° _____


PLANO

PISCINA, VESTIDORES Y RELAJO

2.ª ETAPA (D.S. 007-2003-SA)

ESCALA	FECHA
INDICADA	**NOVIEMBRE 2026**

ESPECIALIDAD	LÁMINA
ARQUITECTURA	**A-08** 8 de 10

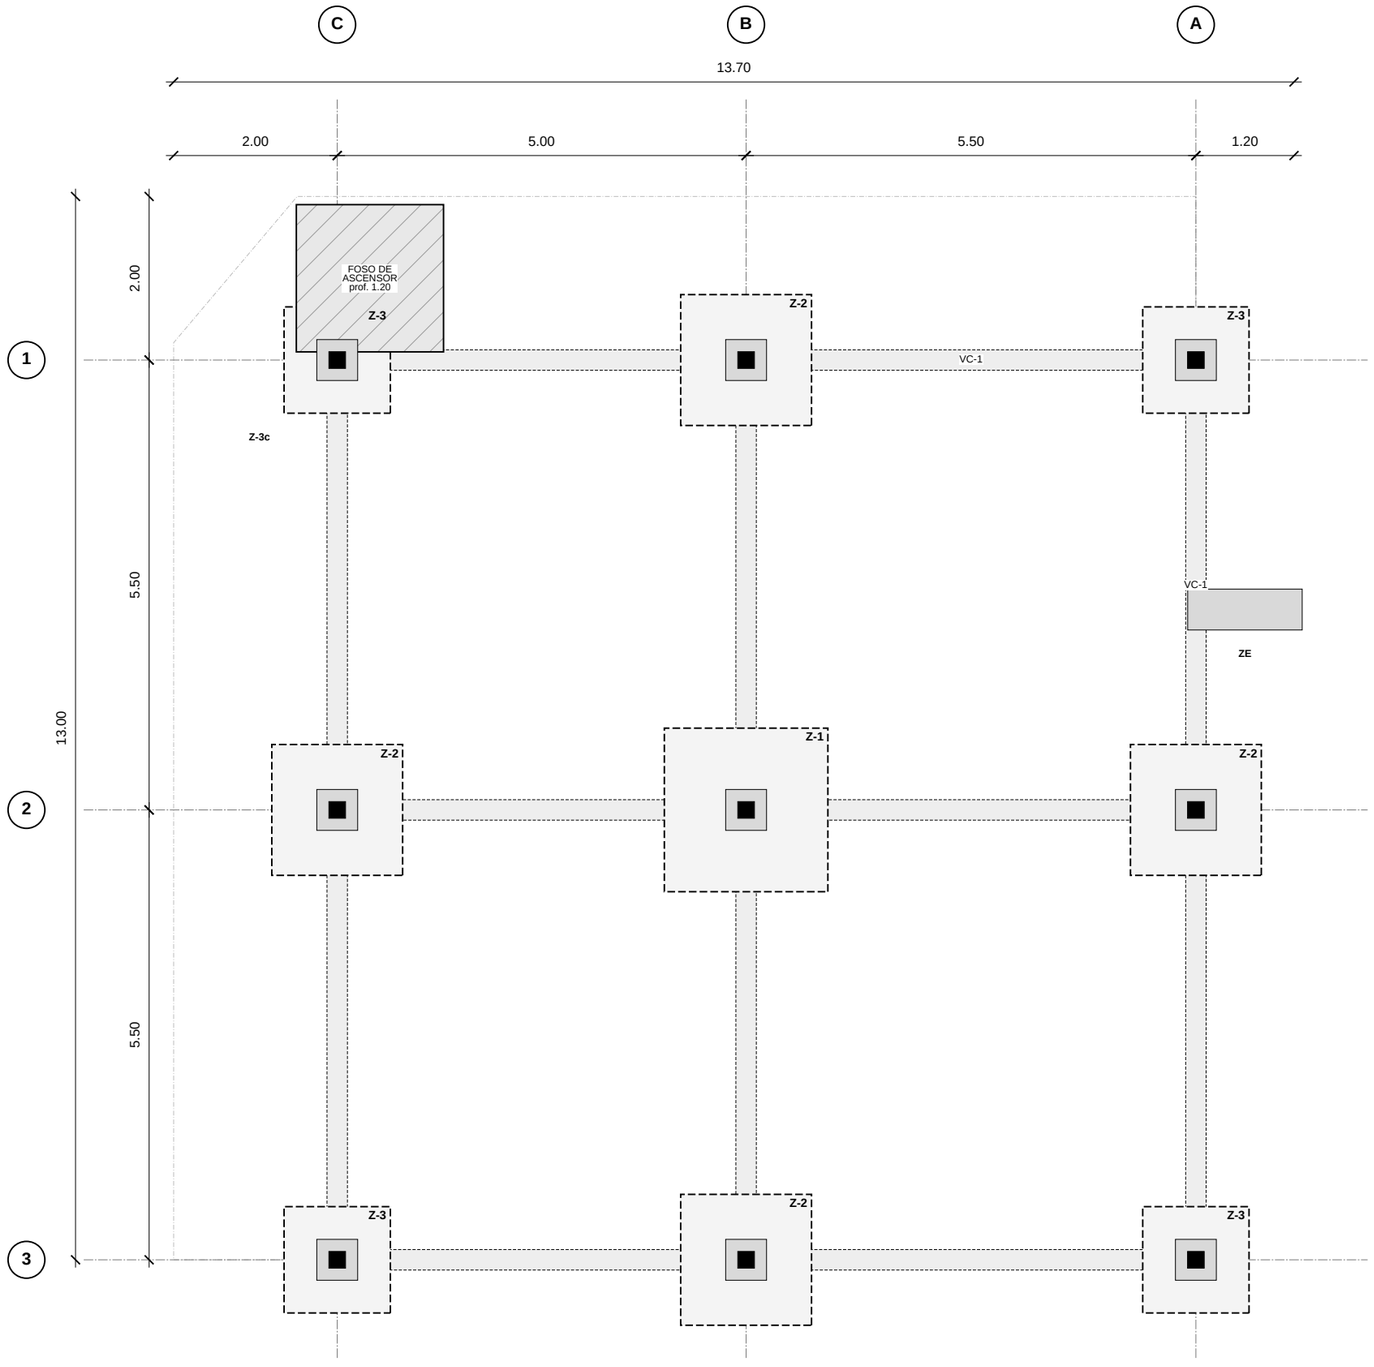


PLANTA DE CIMENTACIÓN

ESC. 1/75

0 1 2 3 4 5 m

DETALLE TÍPICO DE ZAPATA Z-1

ESC. 1/40

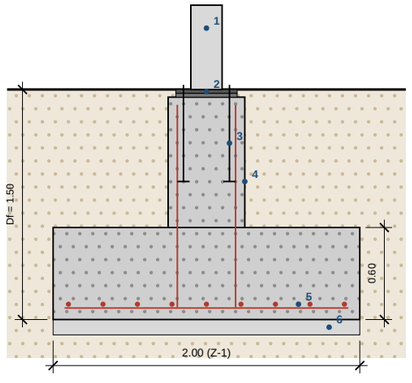

1. Columna HSS 8x8x1/4
2. PL 400×400×25 + grout 25 mm
3. 4 pernos Ø 3/4" L = 0.60 m
4. Pedestal 0.50×0.50, 8 Ø 5/8"
5. Malla Ø 5/8" @ 0.20 (2 direcc.)
6. Solado e = 0.10 m

N

CUADRO DE ZAPATAS

COD.	TIPO	B × L (m)	h (m)	P (kN)	CANT.
Z-1	interior	2.00 × 2.00	0.60	358	1
Z-2	borde	1.60 × 1.60	0.50	231	4
Z-3	esquina	1.30 × 1.30	0.50	139	4

ESPECIFICACIÓN	VALOR
Concreto zapatas, pedestales, VC	f'c = 210 kg/cm²
Solado	f'c = 100 kg/cm², e = 0.10 m
Acero de refuerzo	fy = 4 200 kg/cm² (ASTM A615 G60)
Recubrimiento zapatas / VC	7.5 cm / 4.0 cm
Viga de cimentación VC-1	0.25 × 0.40, 4 Ø 5/8", est. Ø 3/8"
Pernos de anclaje	ASTM F1554 Gr. 36, Ø 3/4", L = 0.60 m
Capacidad portante (supuesta)	q adm = 1.0 kg/cm²

NOTAS

1. Predimensionamiento de anteproyecto (E.020, E.030, E.050, E.060, E.090). Antes de construir: estudio de mecánica de suelos (EMS) y cálculo estructural firmado por ingeniero civil colegiado.
2. Si el EMS da una capacidad menor o suelos expansivos, recalcular las zapatas o usar platea.
3. ZE: zapata de apoyo de la escalera exterior (0.50 × 1.40 × 0.40 m); la escalera principal se apoya en la viga VC-1 del eje 1. Z-3c: zapata del eje C-1 combinada con el foso del ascensor (según el proveedor).
4. Cotas de las zapatas centradas en los ejes; nivel de fondo -1.50 m respecto del NPT ±0.00.

PROYECTO

POLLERÍA CAMPESTRE

ANTEPROYECTO - EDIFICIO DE ESTRUCTURA METÁLICA

UBICACIÓN

Jr. Rodríguez de Mendoza esq. calle lateral
Dist. San Nicolás (Mendoza) - Prov. Rodríguez de Mendoza
Departamento de Amazonas - Perú

PROPIETARIO

_____

PROFESIONAL RESPONSABLE (FIRMA Y SELLO)

Arq. / Ing. CIP N.° _____


PLANO

CIMENTACIÓN

ZAPATAS, PEDESTALES Y VIGAS DE CIMENTACIÓN

ESCALA	FECHA
INDICADA	NOVIEMBRE 2026


ESPECIALIDAD	LÁMINA
ESTRUCTURAS	E-01
	9 de 10

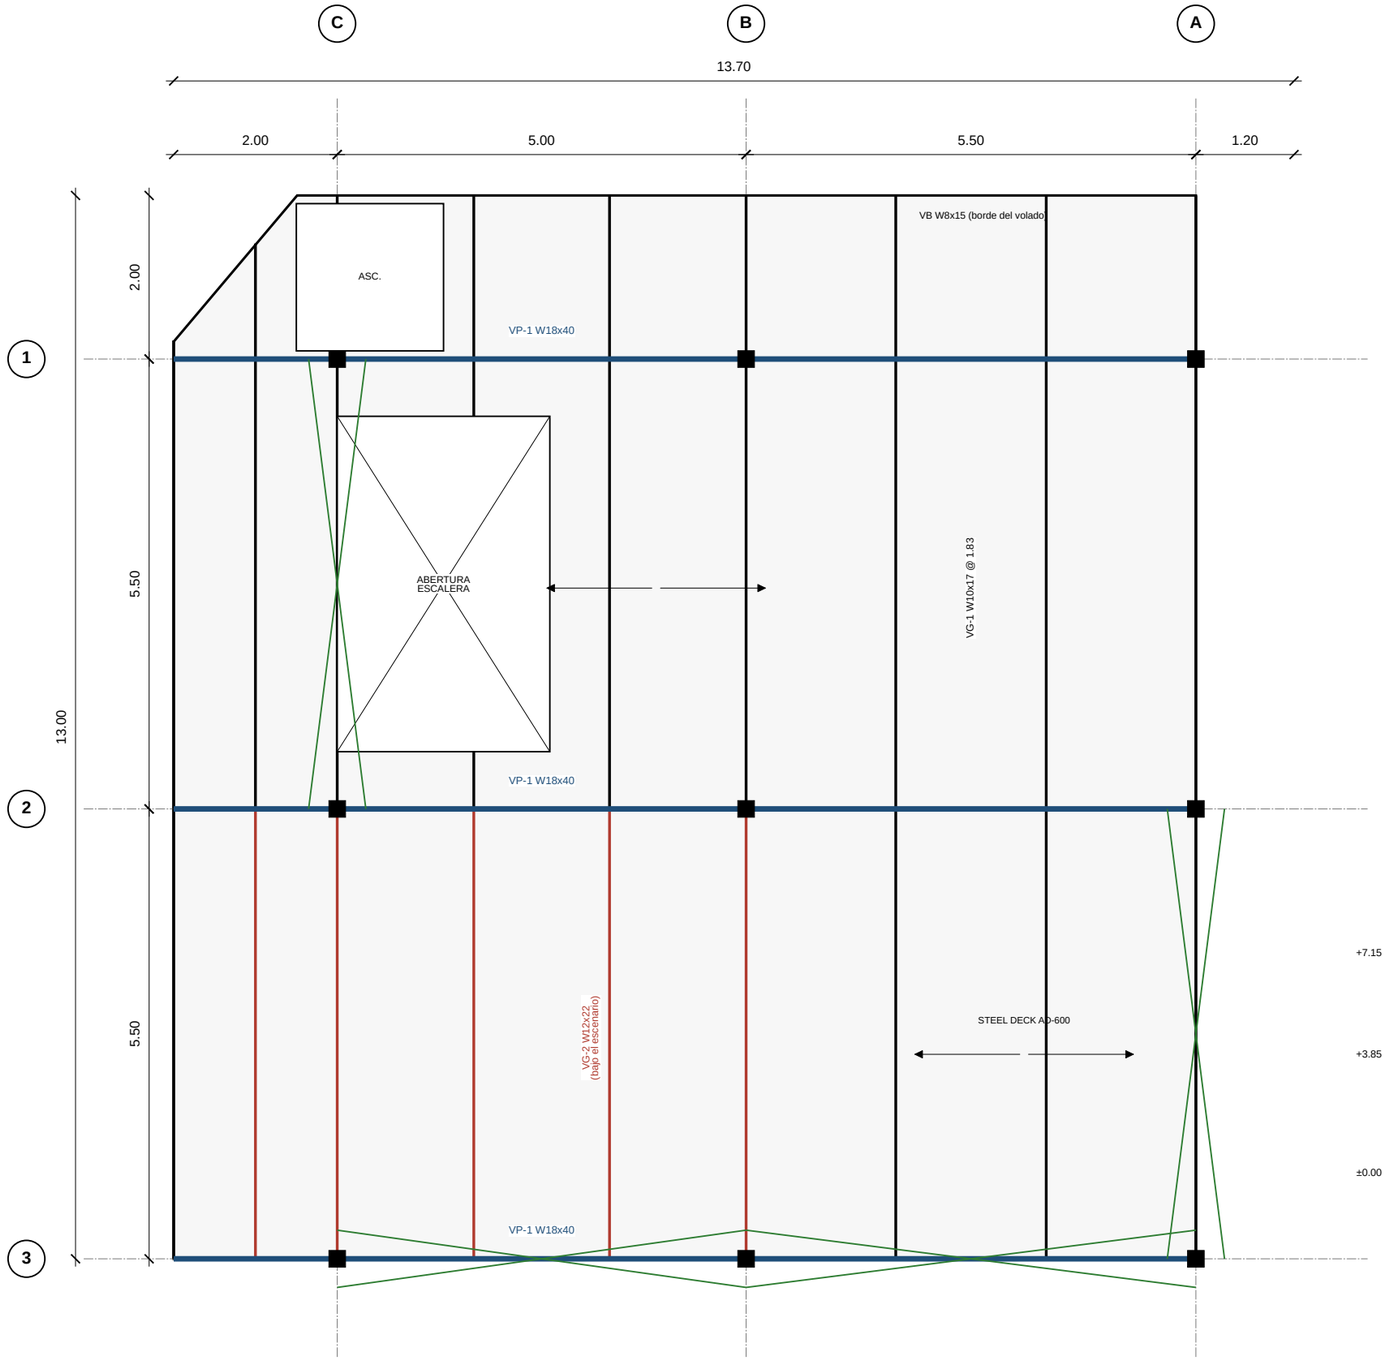

PLANTA DE ENTREPISO +3.85

ESC. 1/75

0 1 2 3 4 5 m

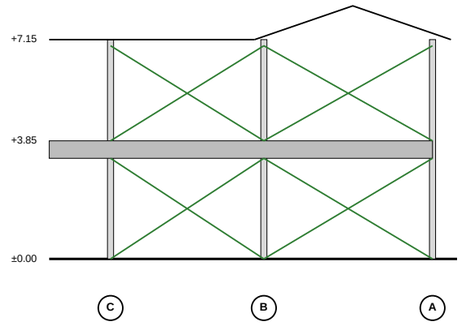

PÓRTICO ARRIOSTRADO - EJE 3

ESC. 1/200

N

CUADRO DE SECCIONES

ELEMENTO	SECCIÓN	MATERIAL
Columnas	HSS 8x8x1/4	ASTM A500 Gr. C
VP-1 vigas principales	W18x40	ASTM A572 Gr. 50
VG-1 viguetas	W10x17	ASTM A572 Gr. 50
VG-2 viguetas (escenario)	W12x22	ASTM A572 Gr. 50
VB vigas de borde	W8x15	ASTM A572 Gr. 50
Arriostres en X	HSS 4x4x1/4	ASTM A500 Gr. C
Vigas de techo	W8x13	ASTM A572 Gr. 50
Correas	C 150×50×15×2.5	ASTM A653
Losa	AD-600 + 12 cm	f'c 210 kg/cm²

PREDIMENSIONAMIENTO (LRFD)

Losa colaborante: Steel deck AD-600 cal. 20 + concreto f'c 210 kg/cm², e = 12 cm; luz 1.83 m

Viguetas: W10x17 @ 1.83 m, L = 5.50 m (uso 82 %, flecha 13 mm ≤ 15); bajo el escenario W12x22

Vigas principales: W18x40, L = 5.50 m + volado 2.00 m (uso 89 %)

Columnas: HSS 8x8x1/4, Pu = 518 kN, φPn = 1118 kN, interacción 0.76

Arriostres: HSS 4x4x1/4 en X, F = 63 kN, φPn = 373 kN

Sismo: Z 0.35 · U 1.3 · C 2.5 · S 1.15 / R 7 = 0.187; P = 996 kN; V = 186 kN

Zapatas: interior 2.0 × 2.0 m, borde 1.6 m, esquina 1.3 m; q adm supuesta 1.0 kg/cm²

Acero estructural: 14,979 kg (93 kg por m² de entrepiso)

NOTAS

1. Cargas: muerta de losa 3.55 kPa + tabiquería 0.5 kPa; viva de terraza 4.0 kPa y de escenario 7.5 kPa (E.020), esta última en vigas, columnas y zapatas.
2. Sismo (E.030): sistema de pórticos arriostrados concéntricos (R = 7), del lado seguro con Z = 0.35 y U = 1.3 hasta confirmar la zonificación vigente.
3. Conexiones atornilladas ASTM A325 y soldadura E70XX; pintura epóxica de 2 capas y esmalte de acabado.
4. Arriostres en planta (verde): eje 3 (A-B y B-C), eje A (2-3) y eje C (1-2) en el 1.er piso; en el 2.º piso el del eje A pasa al paño 1-2.

PROYECTO

POLLERÍA CAMPESTRE

ANTEPROYECTO - EDIFICIO DE ESTRUCTURA METÁLICA

UBICACIÓN

Jr. Rodríguez de Mendoza esq. calle lateral
Dist. San Nicolás (Mendoza) - Prov. Rodríguez de Mendoza
Departamento de Amazonas - Perú

PROPIETARIO

_____

PROFESIONAL RESPONSABLE (FIRMA Y SELLO)

Arq. / Ing. CIP N.° _____

PLANO

ESTRUCTURA METÁLICA

ENTREPISO +3.85, ARRIOSTRES Y PÓRTICO DEL EJE 3

ESCALA	FECHA
INDICADA	**NOVIEMBRE 2026**

ESPECIALIDAD	LÁMINA
ESTRUCTURAS	**E-02** 10 de 10